


B4

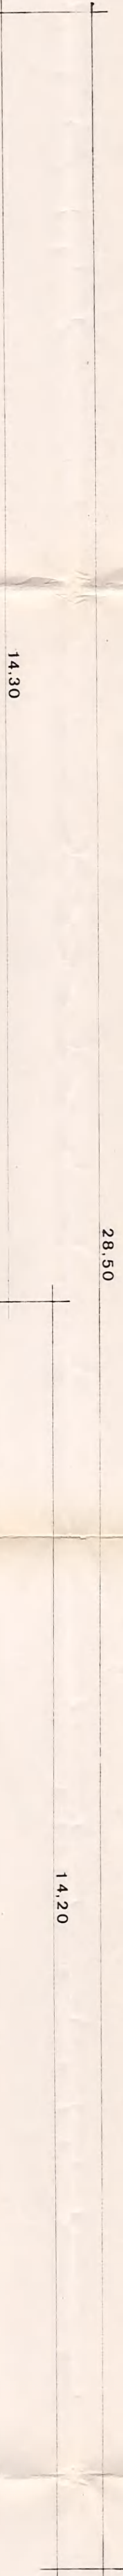

APPARTAMENTO Y

L ₁	=	mq.	17.63
L ₂	=	"	18.49
L ₃	=	"	14.76
K	=	"	13.91
B	=	"	6.60
BS.	=	"	4.93
D	=	"	4.66
I	=	"	17.10
S	=	"	23.22

SUP. UTILE = mq. 121.30

APPARTAMENTO X

L ₁	=	mq.	16.77
L ₂	=	"	18.49
L ₃	=	"	17.63
K	=	"	16.24
B	=	"	6.60
BS.	=	"	6.30
D	=	"	5.78
I	=	"	7.62
S	=	"	21.62

SUP. UTILE = mq. 117.03

APPARTAMENTO K


L ₁	=	mq.	17.80
L ₂	=	"	18.49
L ₃	=	"	17.63
K	=	"	14.60
B	=	"	6.60
BS.	=	"	4.76
D	=	"	7.11
I	=	"	11.21
S	=	"	21.84

SUP. UTILE = mq. 120.04



località martiri

fog. 58

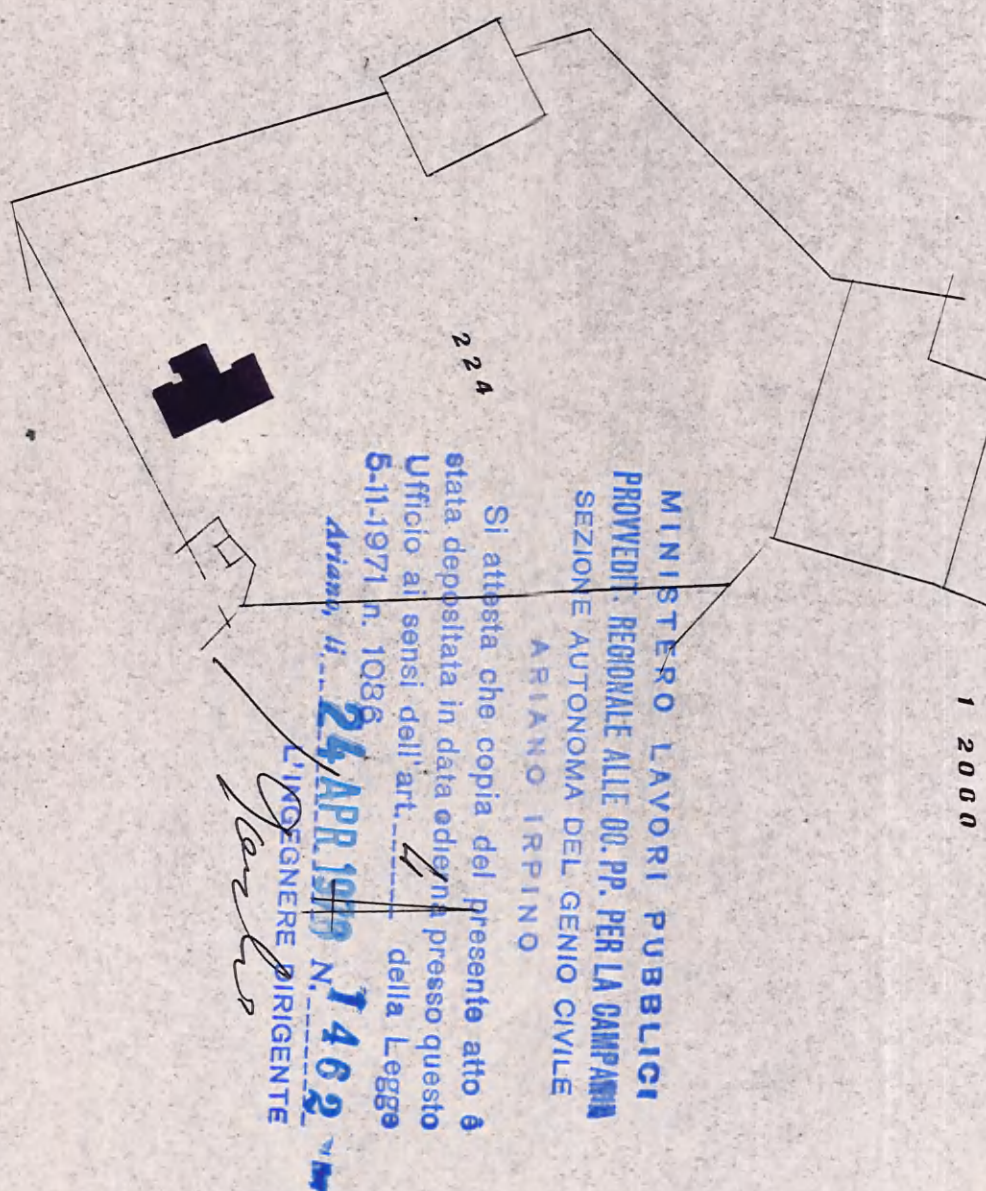

variante
TAV.3 COMUNE ARIANO I. PIA. AVELLINO

PROGETTO per la
costruzione di un fabbricato
per civile abitazione

DITTA: EDILCAL s.r.l.

data rapp. 1:50 piano tipo
il progettista
il collaboratore
geom. G. Riccio

