
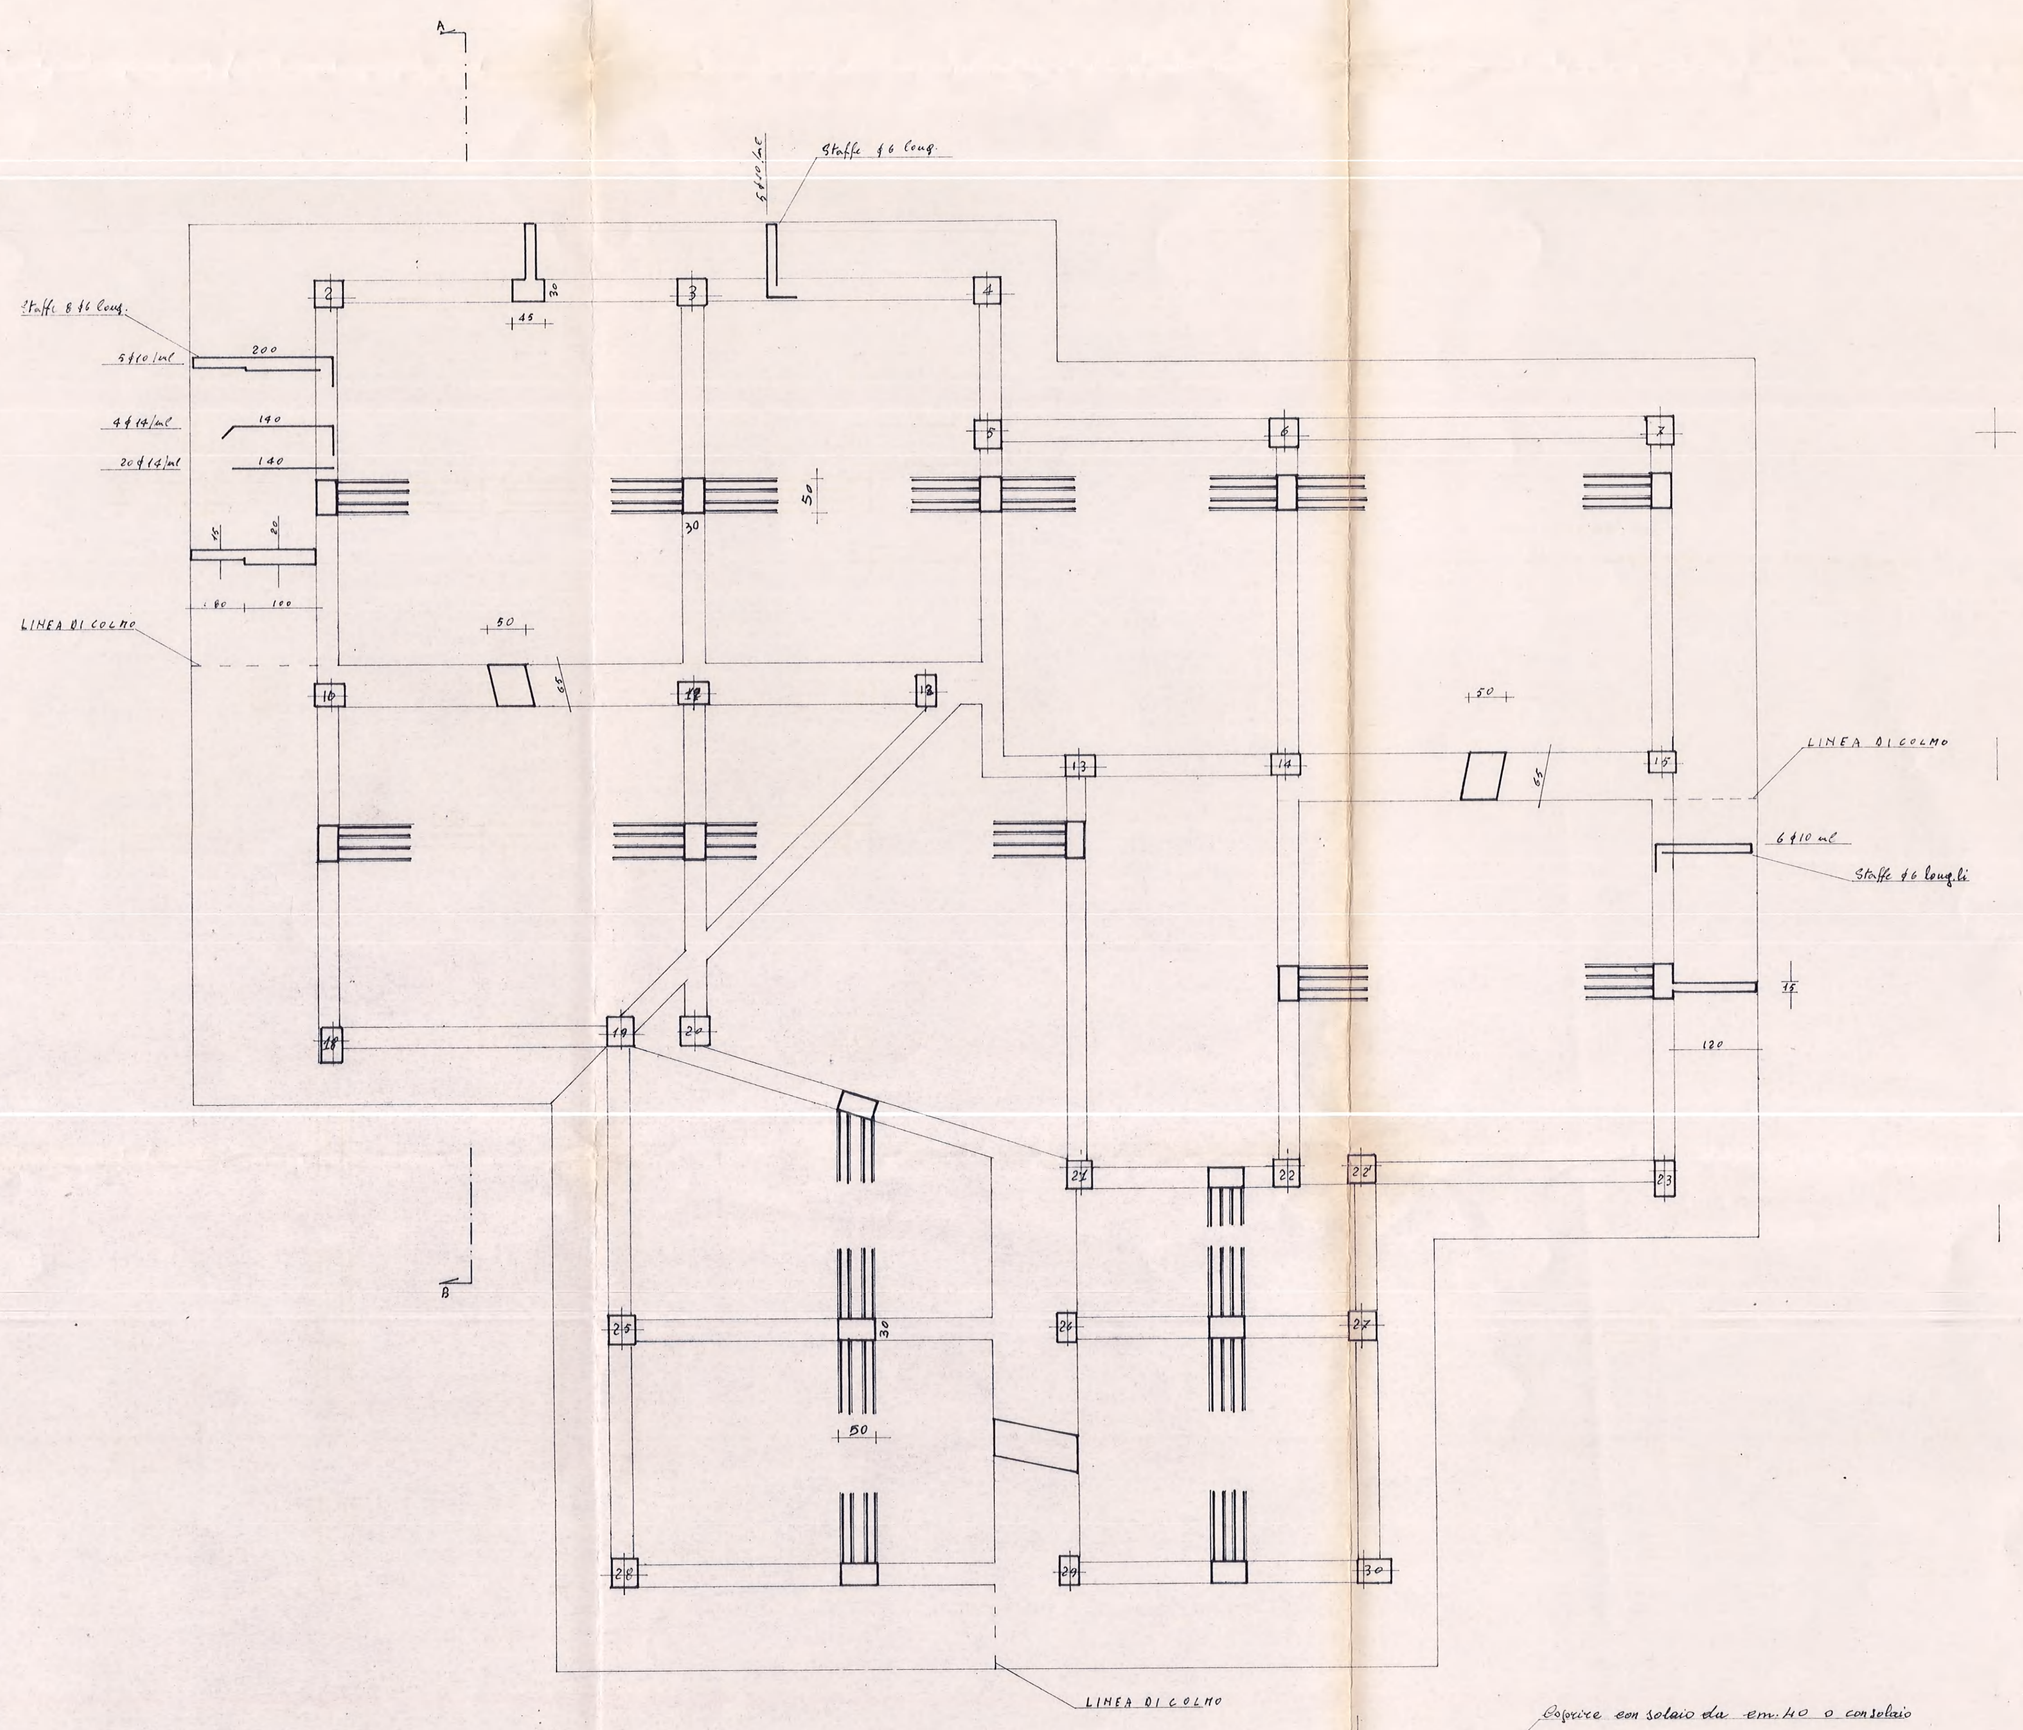


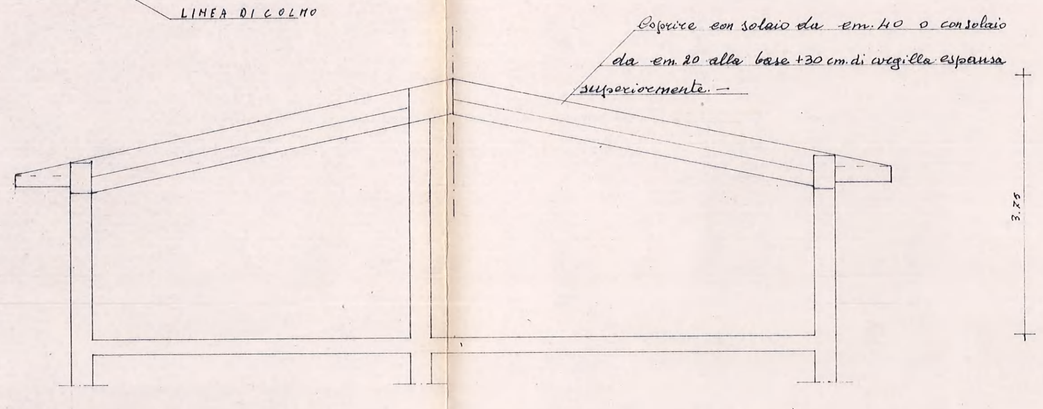

Sezione A-B

località martiri

fog. 58

1 2000



MINISTERO LAVORI PUBBLICI
PROVVEDIT. REGIONALE ALLE OO. PP. PER LA CAMPANIA
SEZIONE AUTONOMA DEL GENIO CIVILE
ARIANO IRPINO
Si attesta che copia del presente atto è stata depositata in data odierna presso questo Ufficio ai sensi dell'art. 4 della Legge 5.11.1971 n. 1086.
Ariano, li 24 APR 1978 N. 1462
L'ADDETTO ALLE PRATICHE

COMUNE **ARIANO I.** prov. AVELLINO

PROGETTO per la costruzione di un fabbricato per civile abitazione

DITTA: EDILCAI srl

TAV. **6** rapp. 1:50

STRUTTURE IN CEMENTO ARMATO
"CARPENTERIA COPERTURA"

IL CALCOLATORE
ing. a. tortorella