località martiri

fog. 15

MINISTERO LAVORI PUBBLICI
PROT. N. 22/2-ALL. N. 81-11 LUGLIO 1966
REGIO DECRETO 16 LUGLIO 1905
N. 1684 E SUCCESSIVE MODIFICHE
SI DICHIARA CHE QUESTA COSTRUZIONE DEVE
ESSERE COSTRUITA IN CONFORMITÀ DELLE
NORME CONTENUTE NEL DECRETO MINISTERIALE
DEL 14 GIU. 1974
Ariano Irpino 24 GIU. 1974
IL FUNZIONARIO DELEGATO

COMUNE **ARIANO I.** prov. AVELLINO

PROGETTO per la costruzione di un fabbricato per civile abitazione

DITTA: **EDILCAI srl**

TAV. **3.4.** sopp. 1:50

STRUTTURE IN CEMENTO ARMATO

IL PROGETTISTA
ing. m. tortoriello

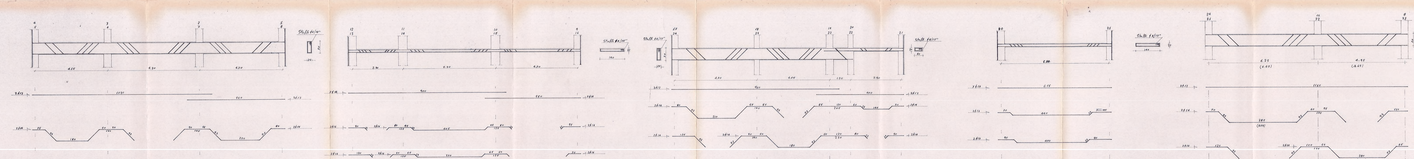
Scala 1:50
Scala 1:100
Scala 1:50
Scala 1:50
Scala 1:50