località **martiri**

fog. 58

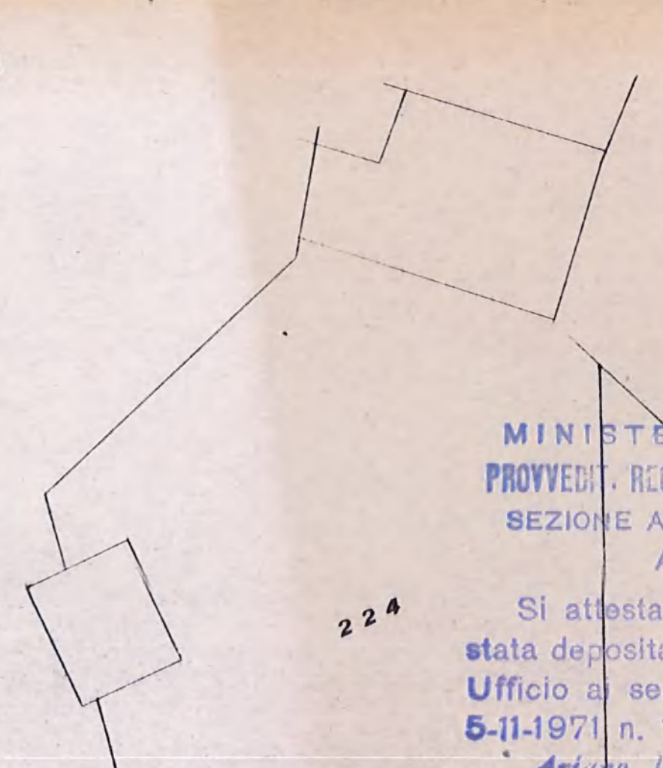

MINISTERO LAVORI PUBBLICI
PROVVEDIT. REGIONALE ALLE OO. PP. PER LA CAMPANIA
SEZIONE AUTONOMA DEL GENIO CIVILE
ARIANO IRPINO

Si attesta che copia del presente atto è stata depositata in data odierna presso questo Ufficio ai sensi dell'art. 4 della Legge 5-11-1971 n. 1086.

Ariano, li 24 APR 1978 N. 1462

L'INGEGNERE DIRIGENTE

COMUNE **ARIANO I.** prov. AVELLINO

PROGETTO per la costruzione di un fabbricato per civile abitazione

DITTA: EDILCAI srl

TAV. **6**A rapp. 1:50

STRUTTURE IN CEMENTO ARMATO
"ARMATURA COPERTURA"

IL CALCOLATORE
ing. a. tortorella

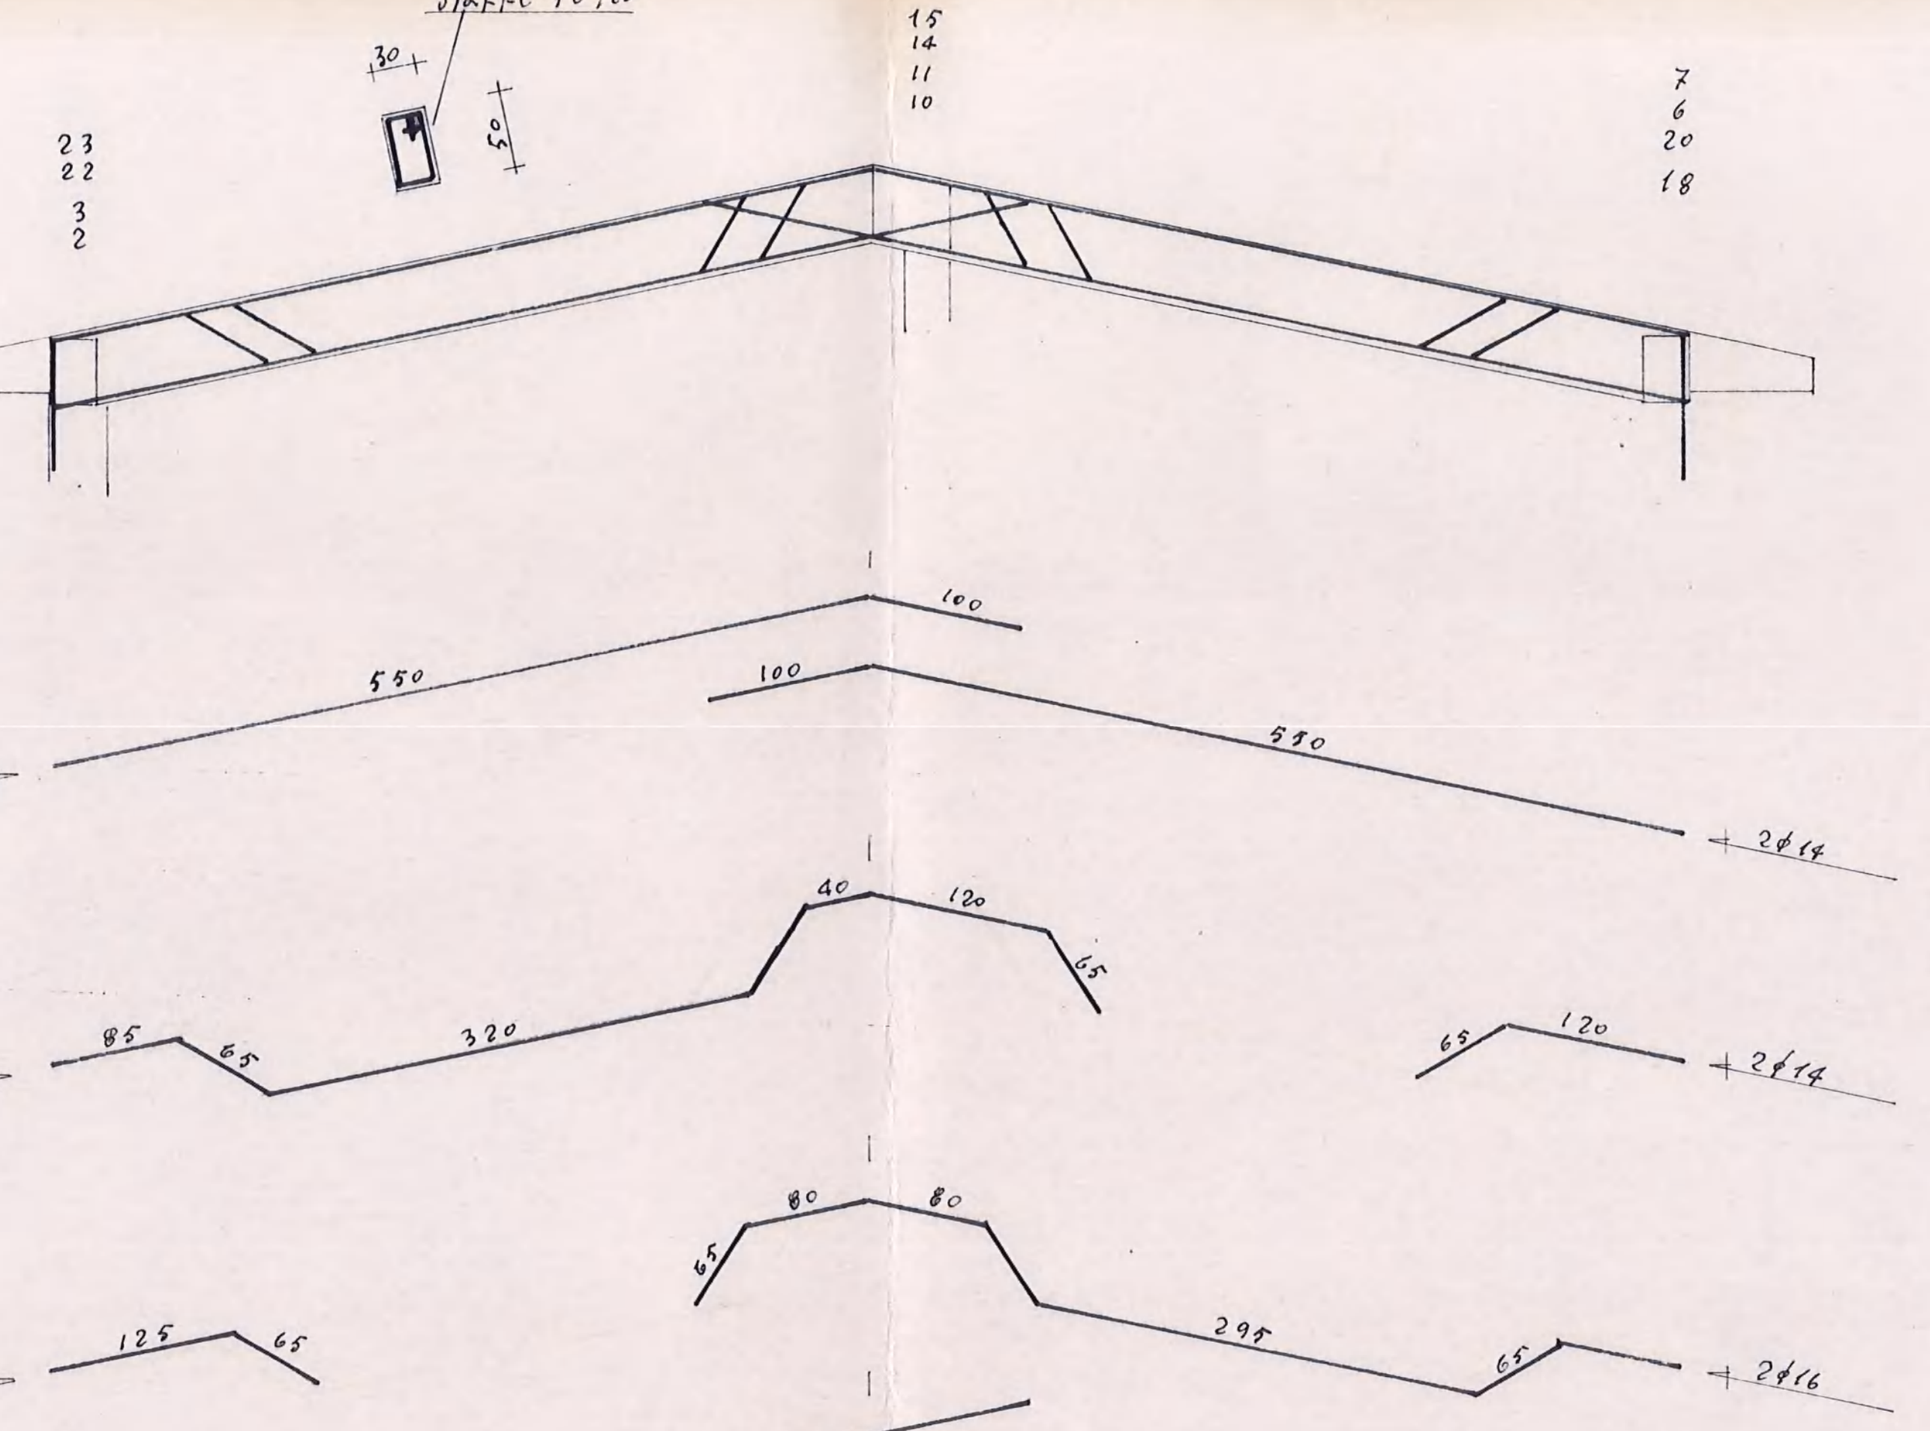
Staffe φ6/20''
30
50
23
22
3
2
15
14
11
10
7
6
20
18
100
550
100
550
2φ14
2φ14
40
120
65
85
65
320
2φ16
65
120
2φ14
80
80
65
125
65
2φ14
295
65
2φ16
550
660
2φ14
2φ14

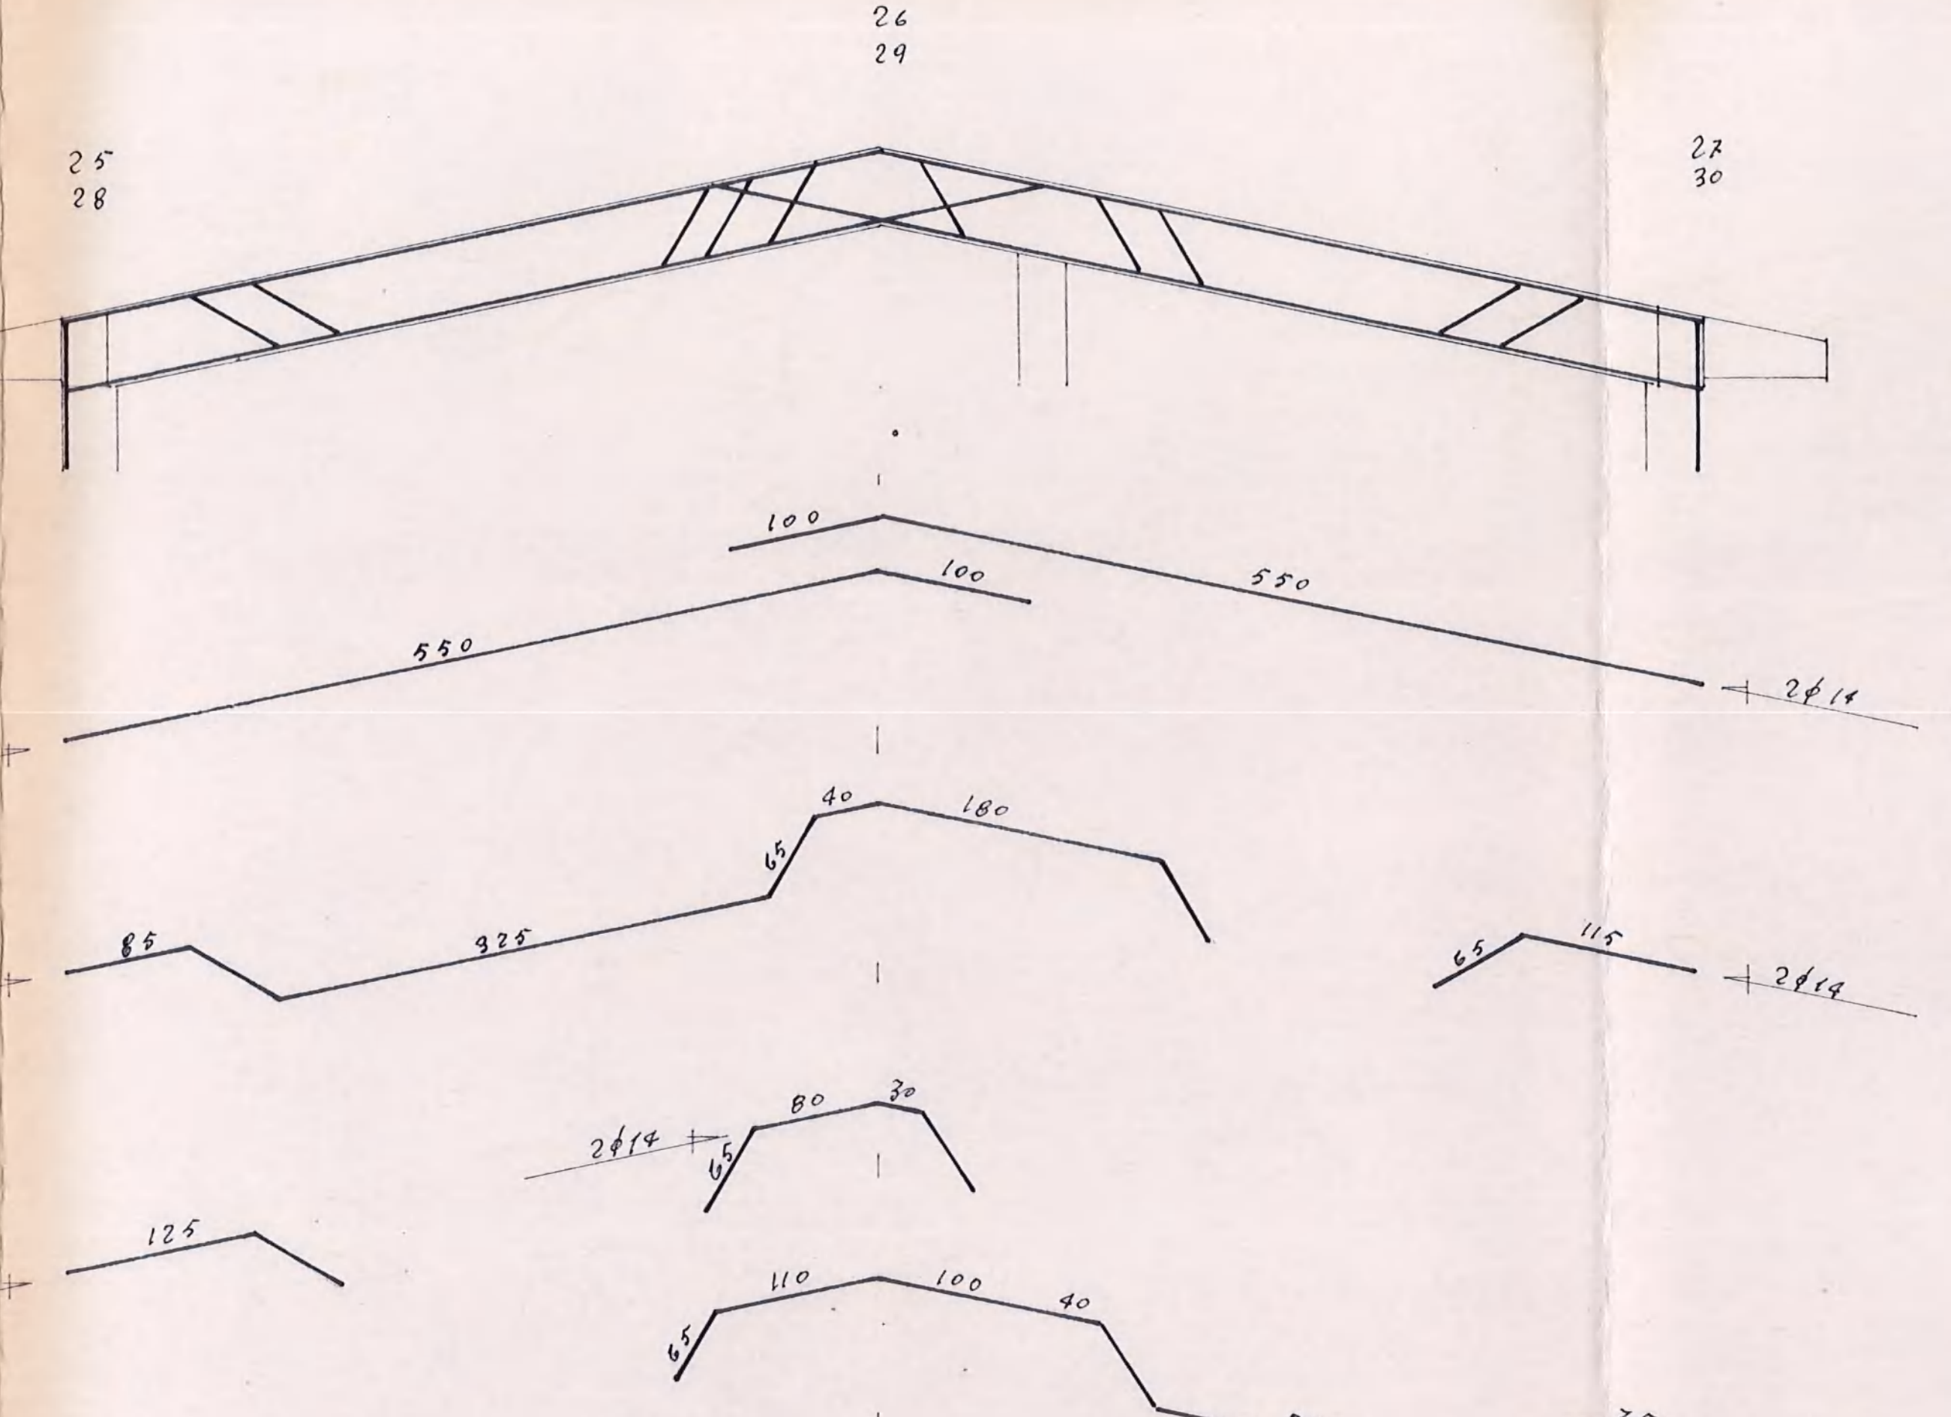
26
29
25
28
27
30
100
100
550
550
2φ14
2φ14
40
180
65
85
325
2φ16
65
115
2φ14
80
30
65
2φ14
125
2φ14
110
100
40
65
230
65
75
2φ14
660
660
2φ14
2φ14

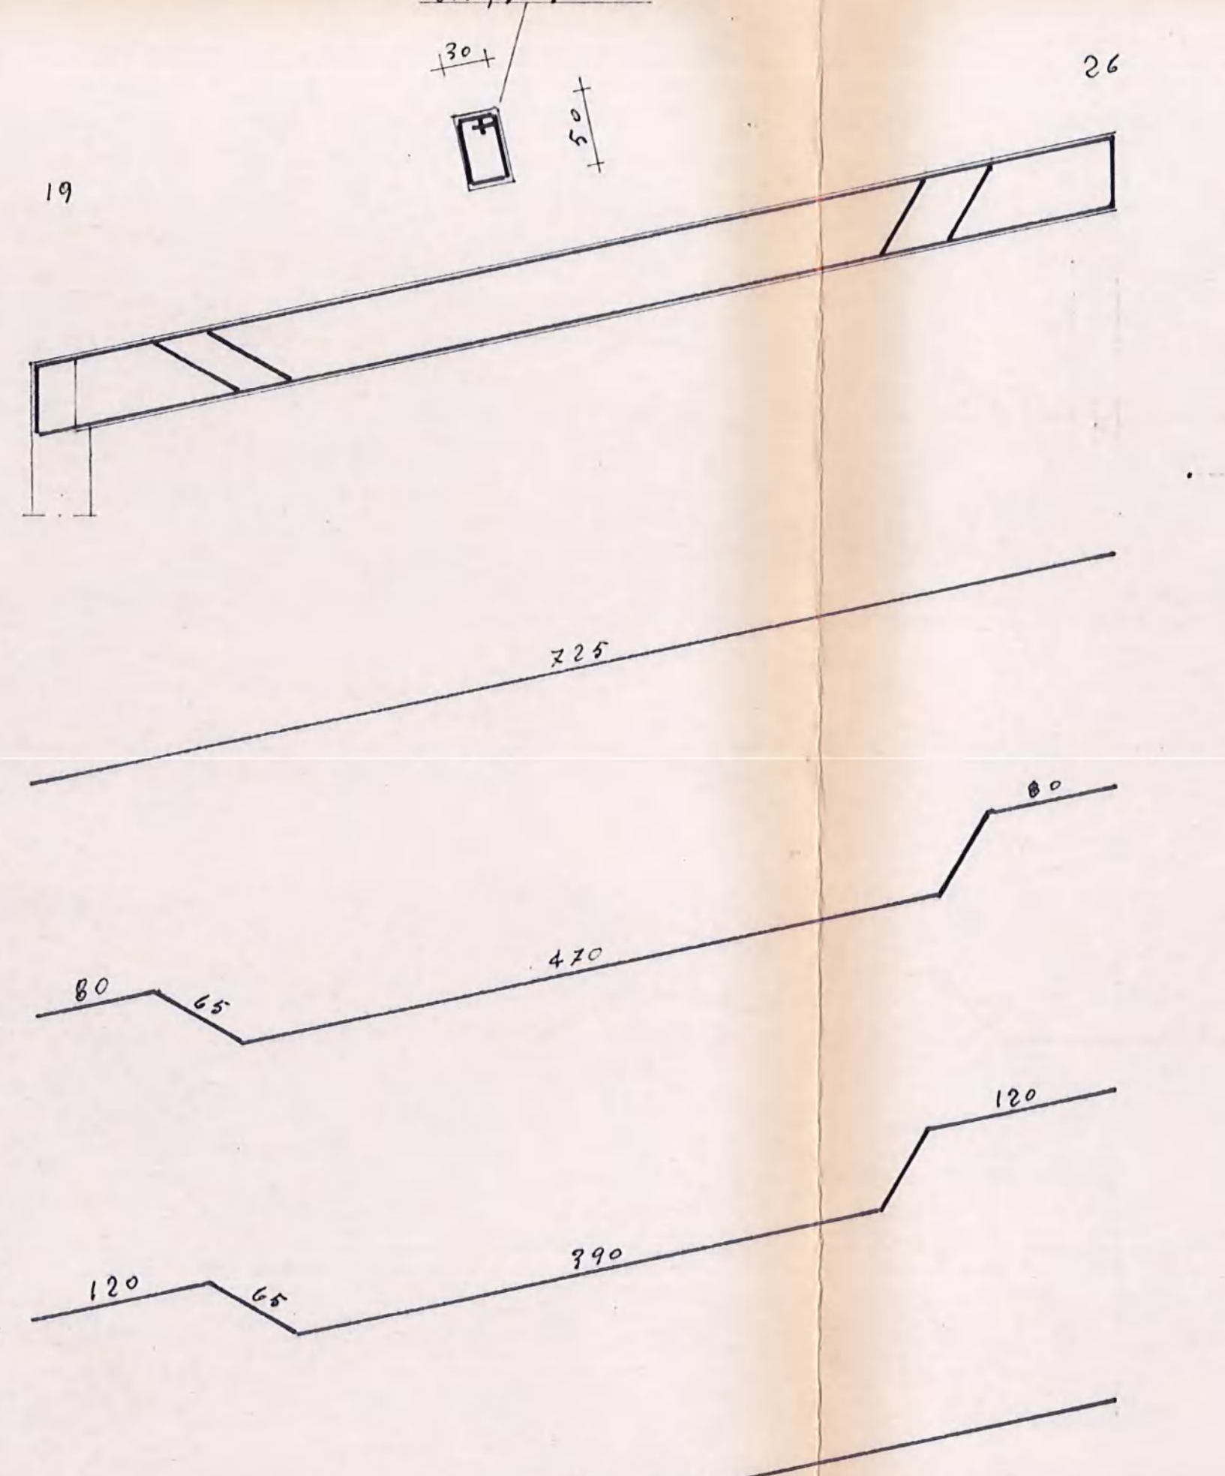
Staffe φ6/15''
30
50
19
26
725
2φ16
80
65
470
80
2φ16
120
65
390
120
2φ16
725
2φ16

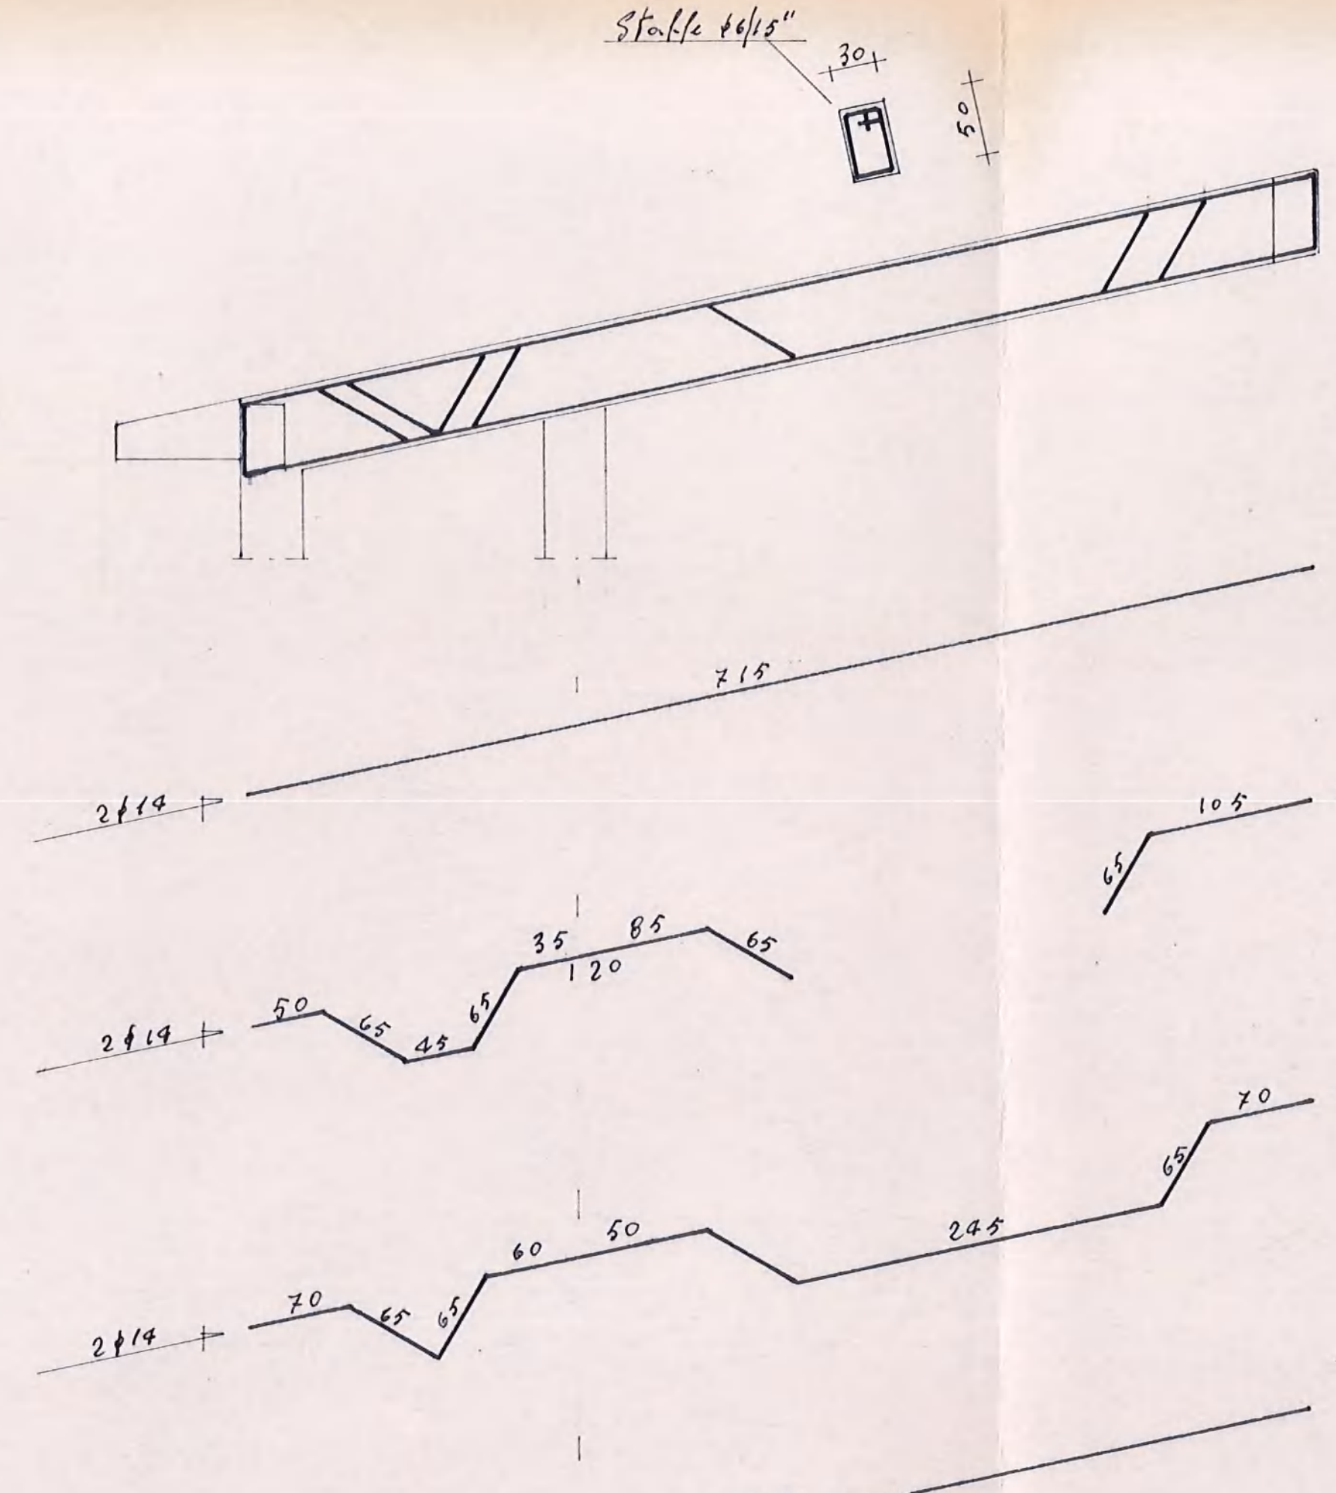
Staffe φ6/15''
30
50
715
2φ14
105
65
2φ14
50
65
45
65
35
120
85
65
2φ14
70
65
65
60
50
245
65
70
2φ14
715
2φ14

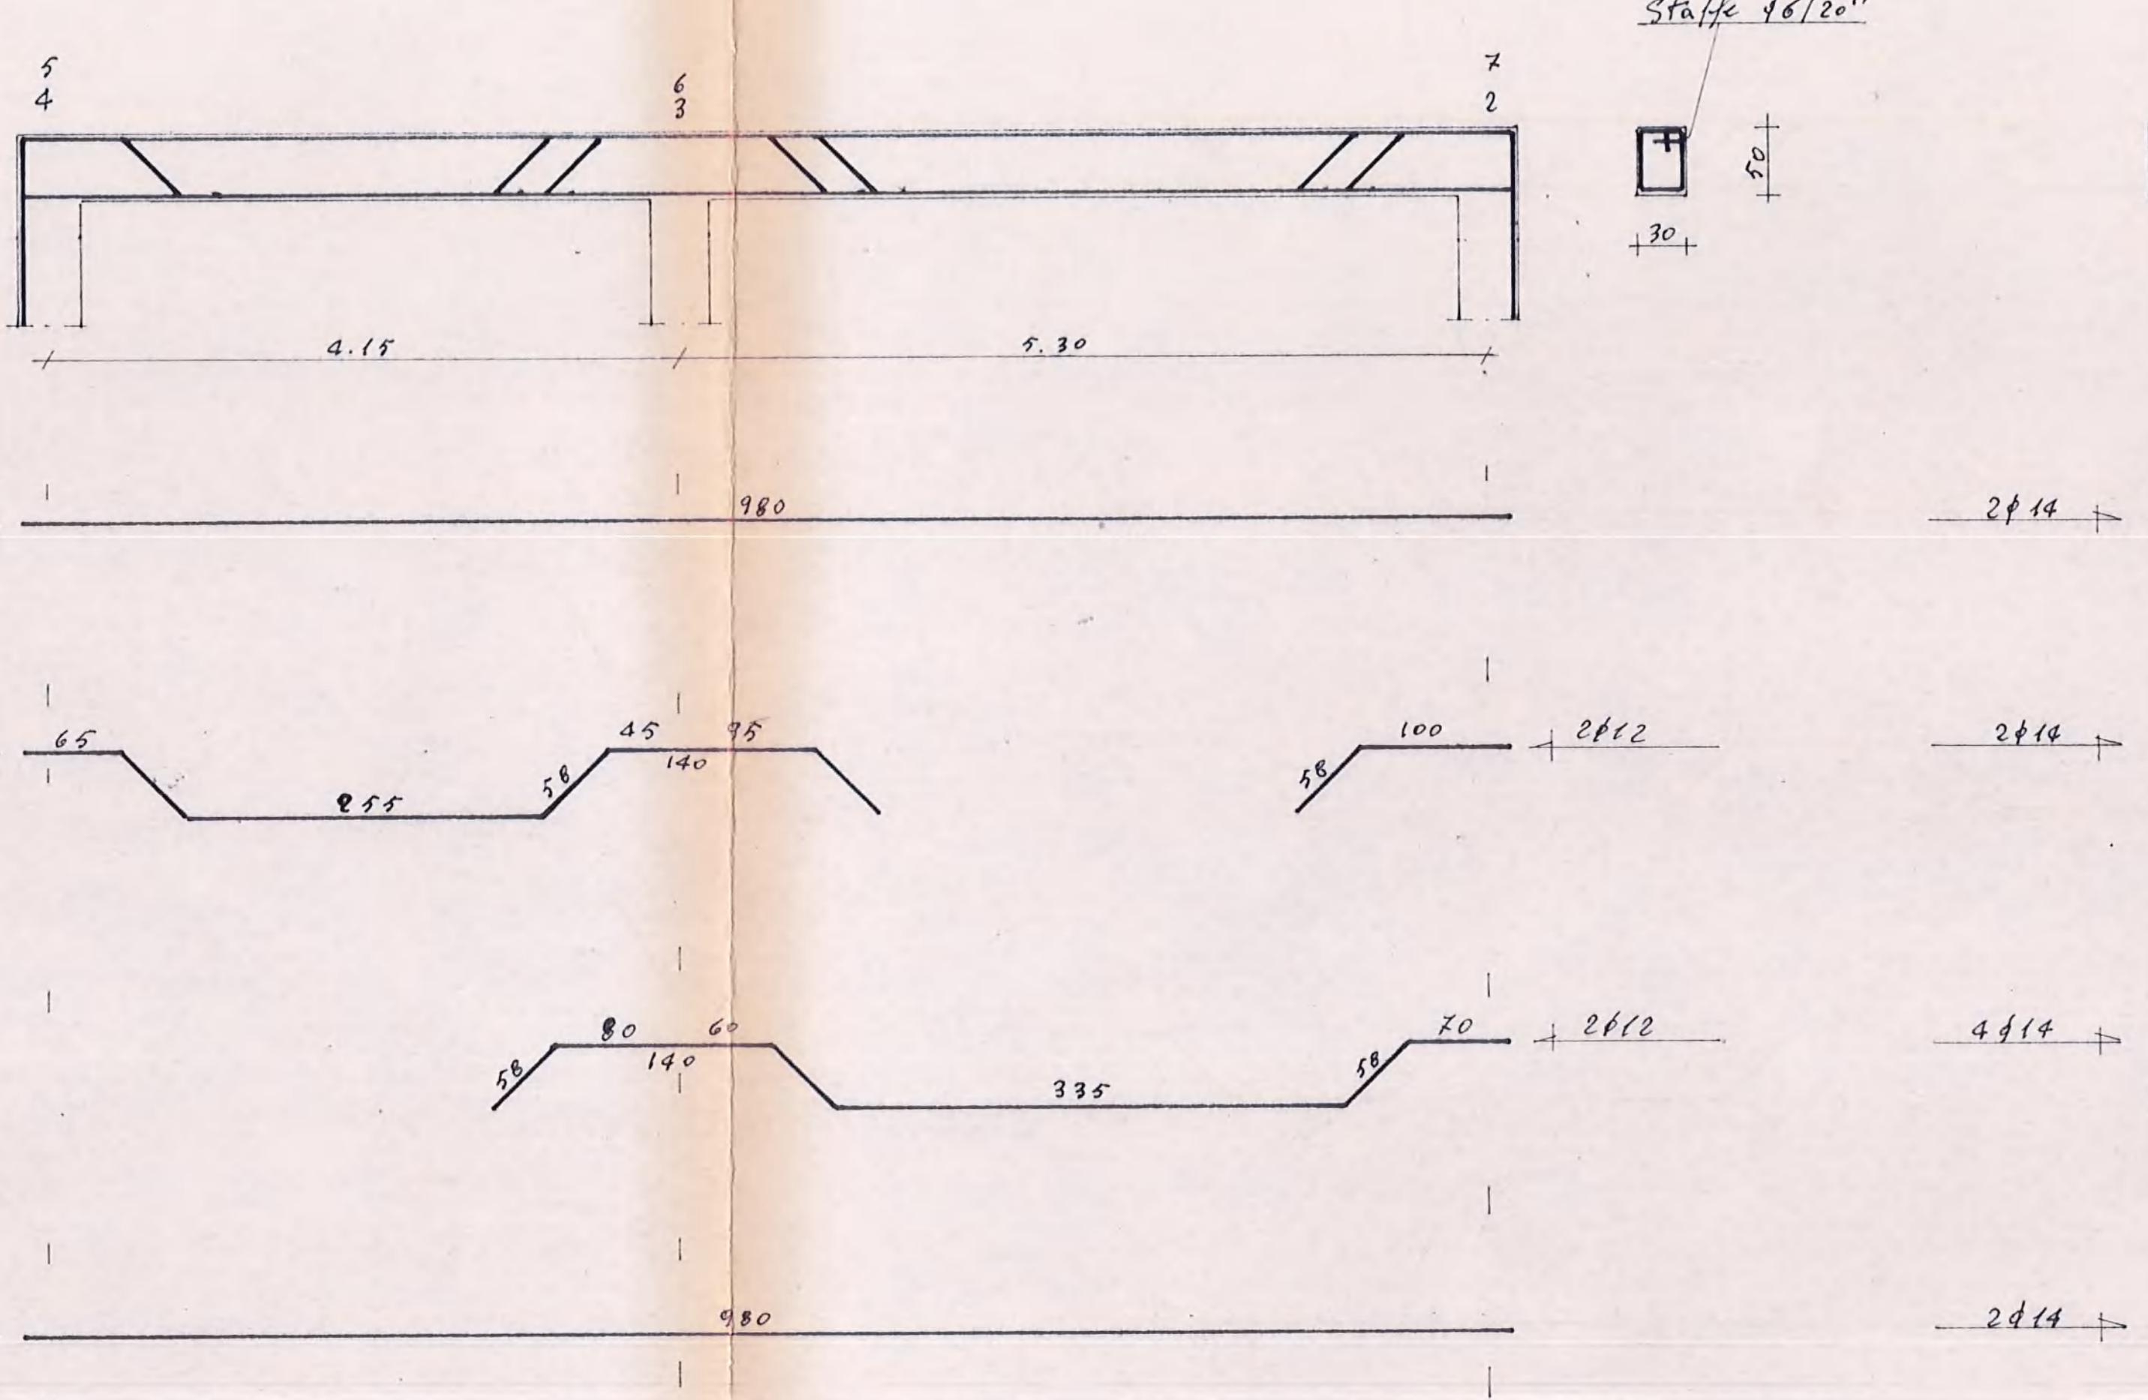
Staffe φ6/20''
50
30
5
4
6
3
7
2
4.15
5.30
2φ12
980
2φ12
65
255
58
45
140
95
58
100
2φ12
58
80
140
60
335
58
70
2φ12
2φ12
980

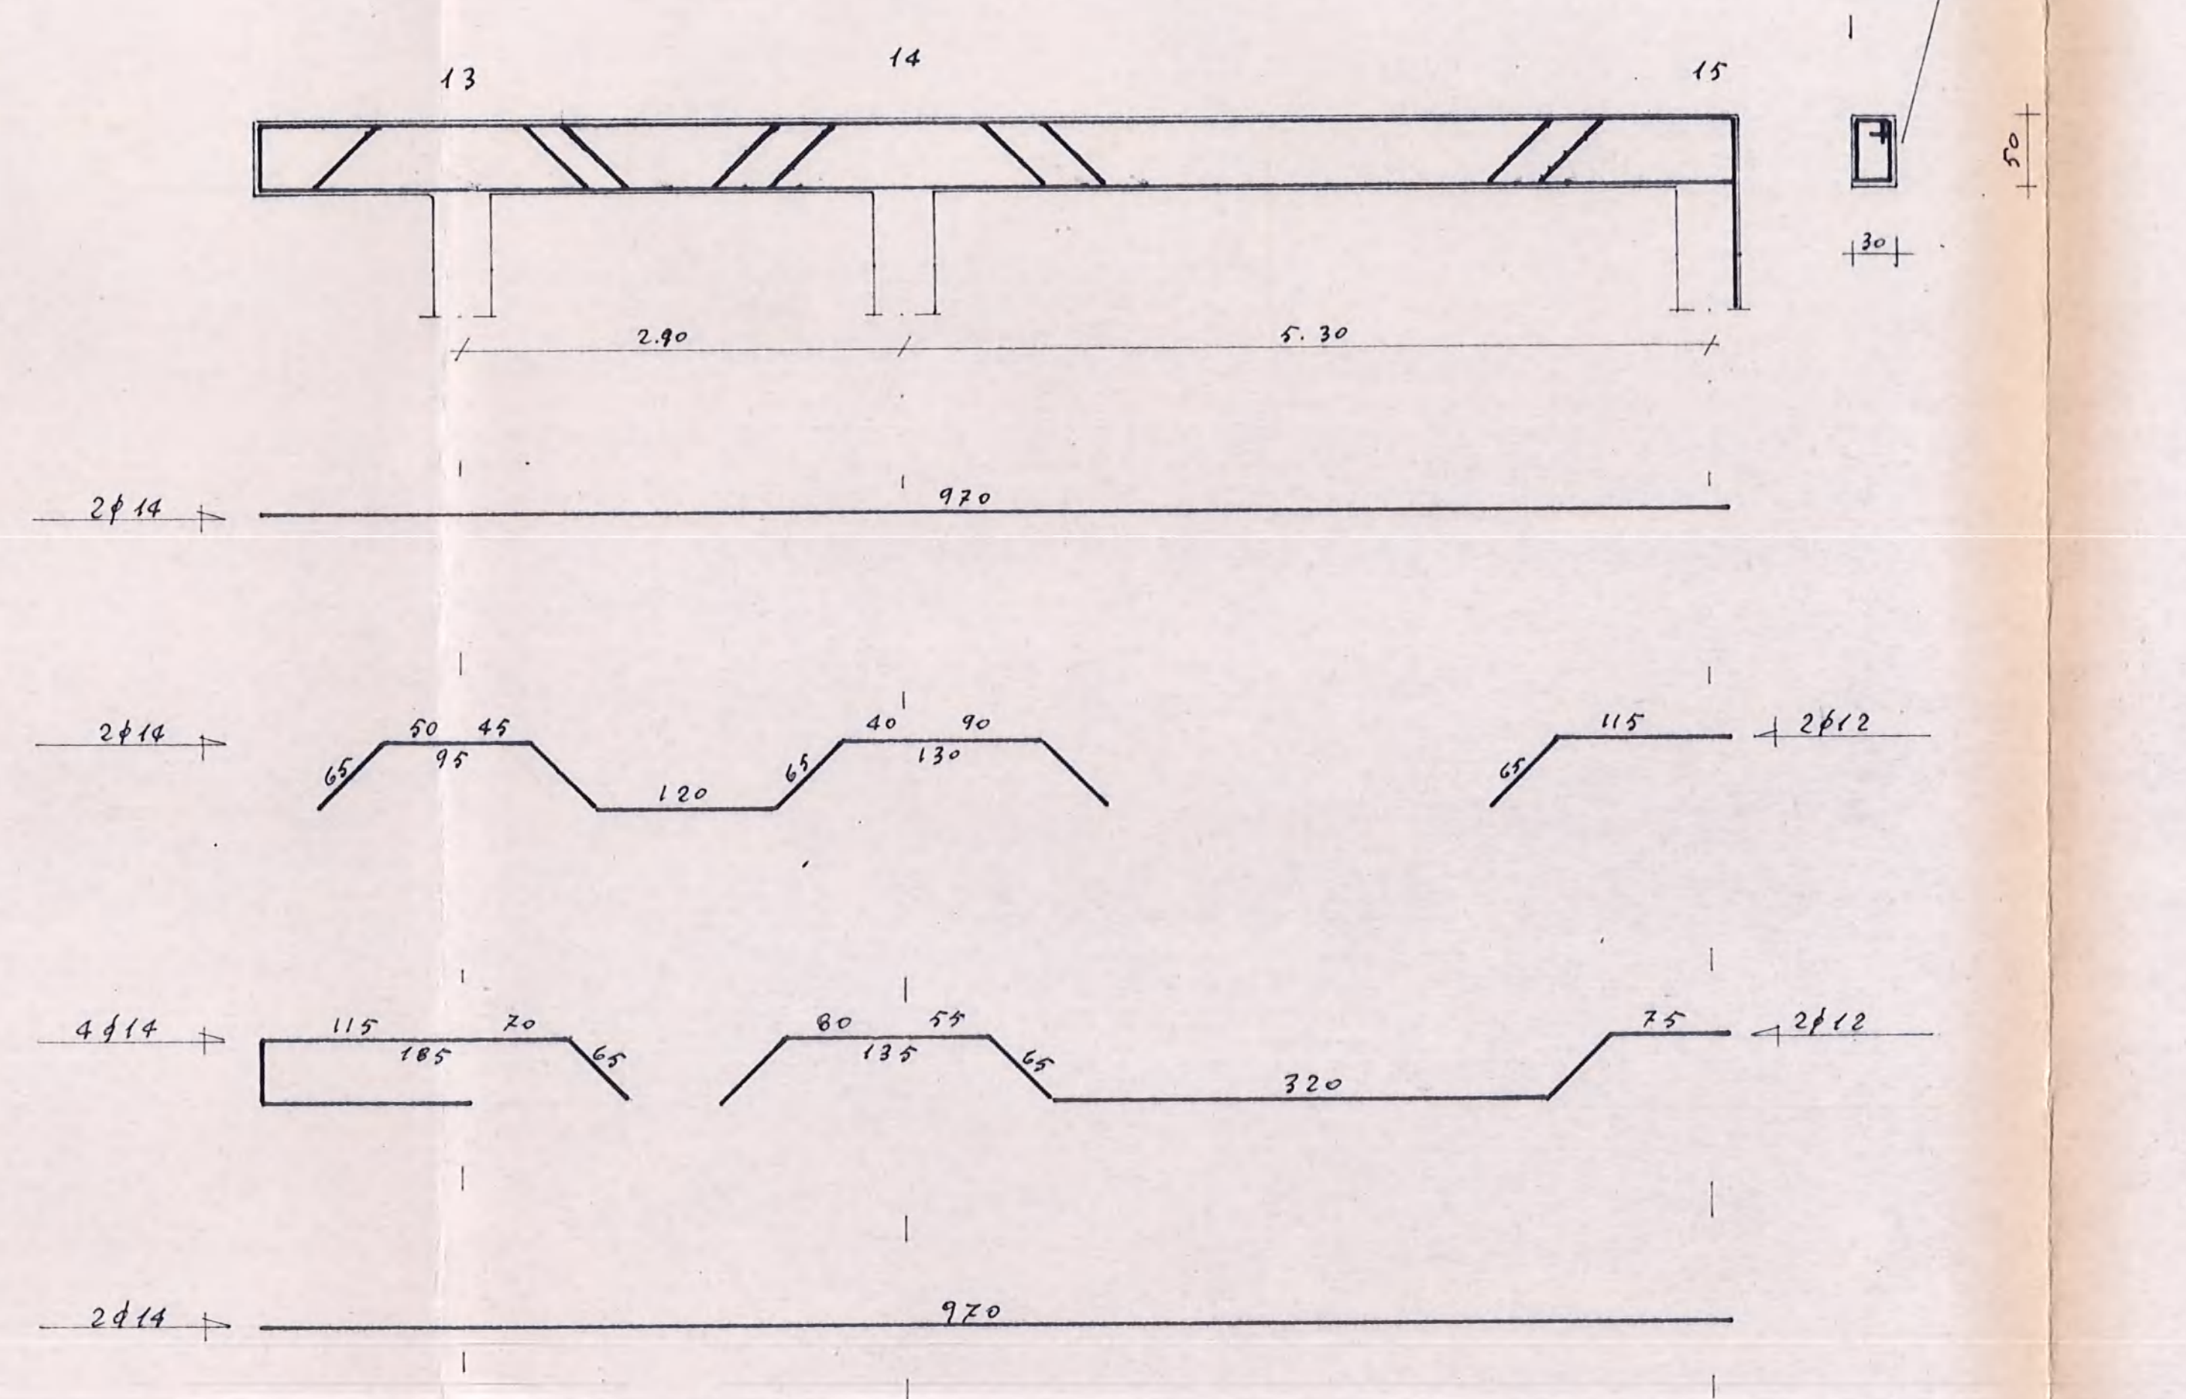
Staffe φ6/20''
50
30
13
14
15
2.90
5.30
2φ14
970
2φ14
65
50
95
45
120
65
40
130
90
65
115
2φ12
4φ14
115
185
70
65
80
135
55
65
320
75
2φ12
2φ14
970