località martiri

fog. 58

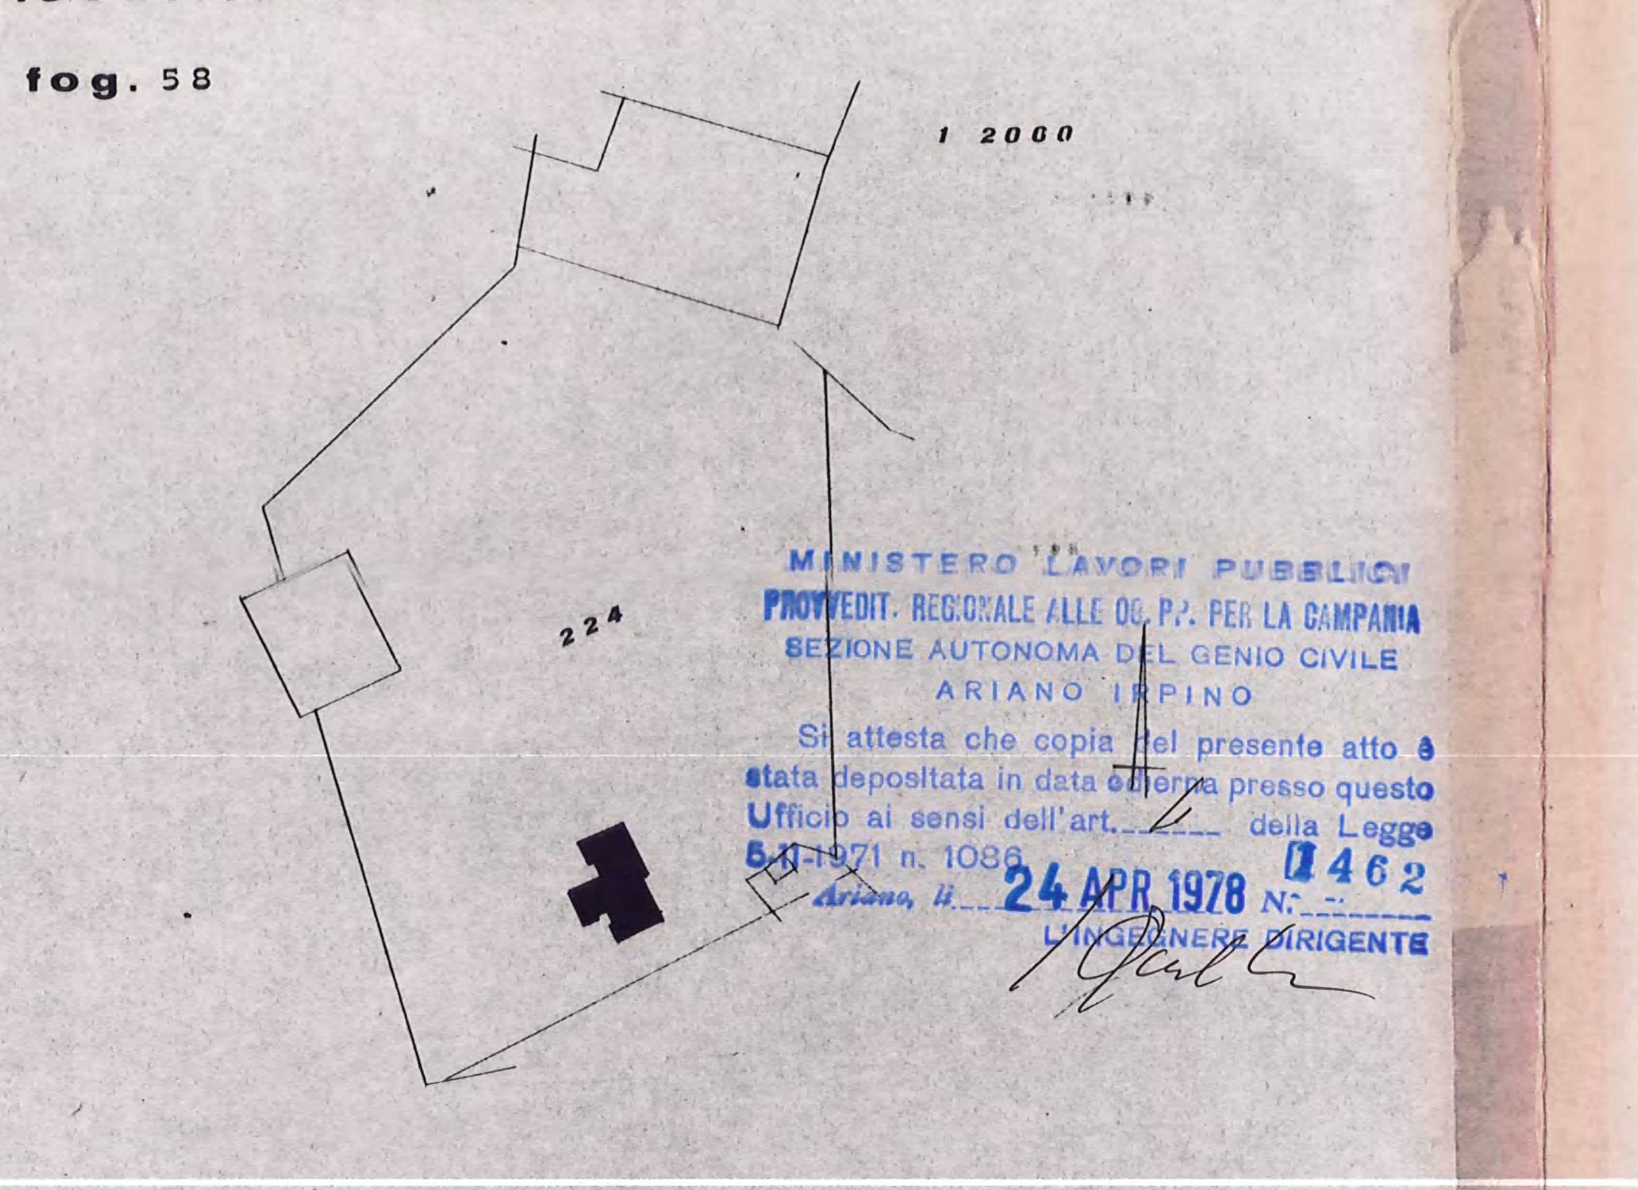

MINISTERO LAVORI PUBBLICI
PROVVEDIT. REGIONALE ALLE OO. PP. PER LA CAMPANIA
SEZIONE AUTONOMA DEL GENIO CIVILE
ARIANO IRPINO
Si attesta che copia del presente atto è stata depositata in data odierna presso questo Ufficio ai sensi dell'art. 4 della Legge 5-11-1971 n. 1086
Ariano, lì 24 APR 1978 N. 0462
L'INGEGNERE DIRIGENTE

COMUNE **ARIANO I.** prov. AVELLINO

PROGETTO per la costruzione di un fabbricato per civile abitazione

DITTA: EDILCAI srl

TAV. **7** rapp. 1:10

STRUTTURE IN CEMENTO ARMATO
"CARPENTERIA E ARMATURA PILASTRI"

IL CALCOLATORE
ing. a. tortorella

Pilastri I° Ordine

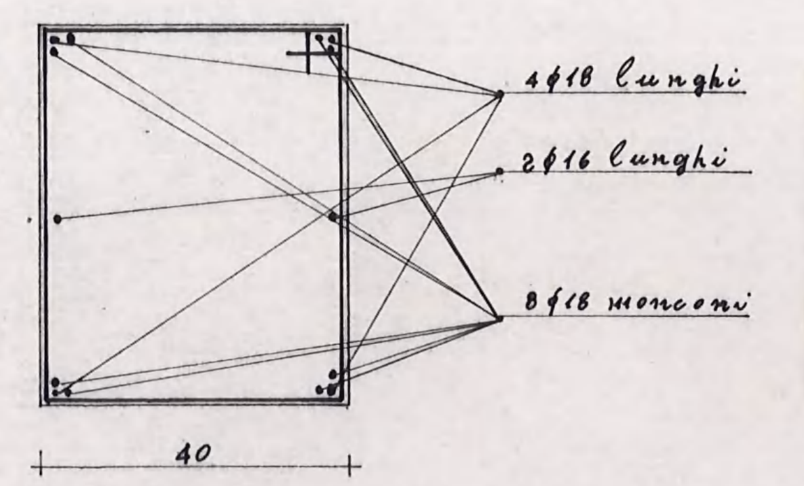
50
40
4φ18 lunghi
2φ16 lunghi
8φ18 monconi

Staffe φ6/20"

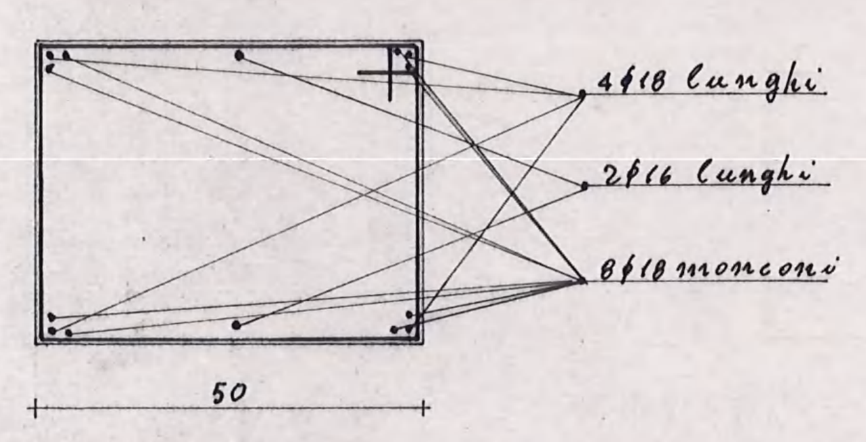
40
50
4φ18 lunghi
2φ16 lunghi
8φ18 monconi

Staffe φ6/20"

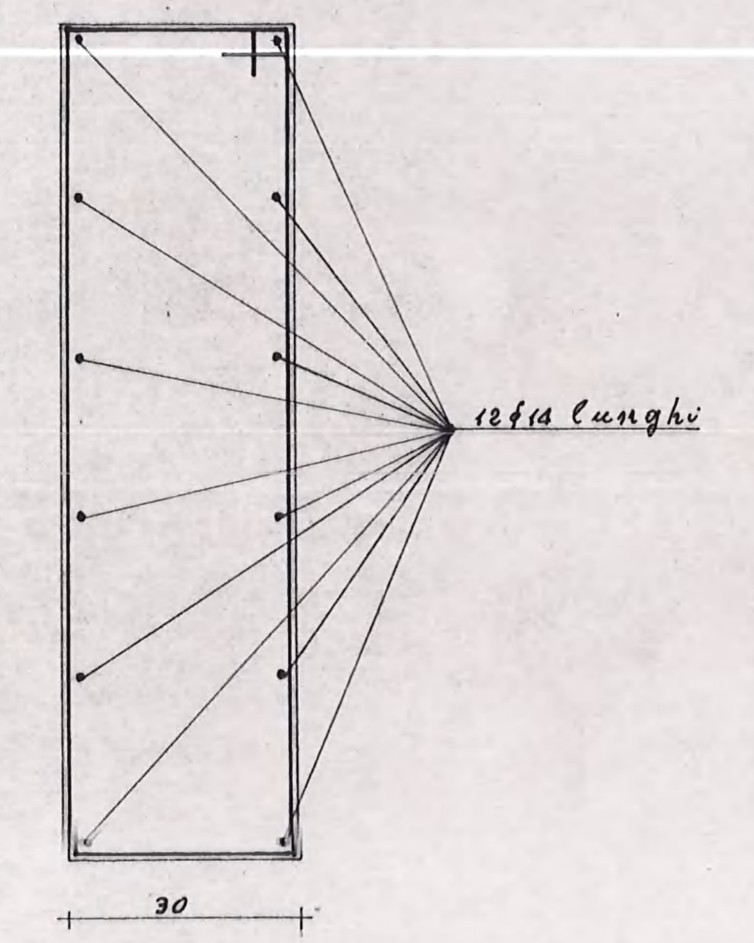
110
30
10φ14 lunghi

Staffe φ6/15"

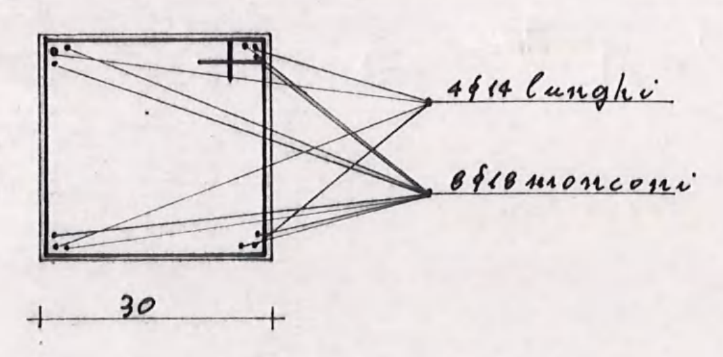
30
30
4φ14 lunghi
8φ18 monconi

Staffe φ6/15"

Pilastri II° Ordine

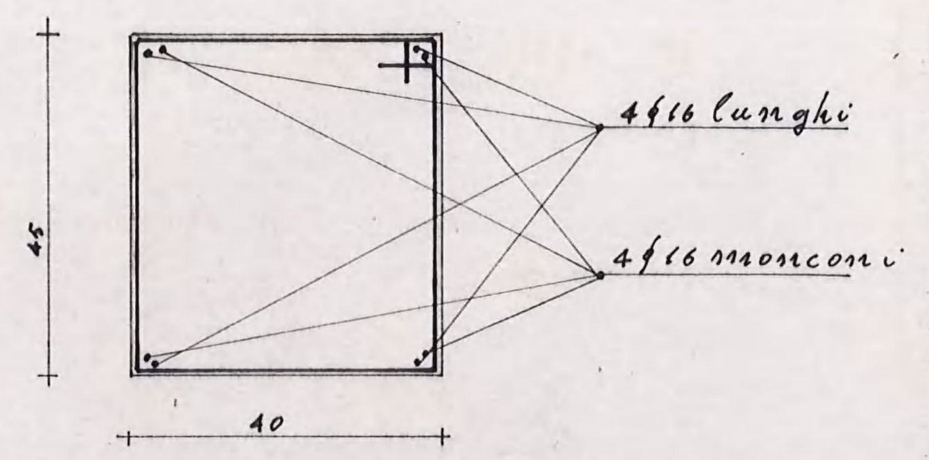
45
40
4φ16 lunghi
4φ16 monconi

Staffe φ6 φ15"

Pilastri 9-16-32

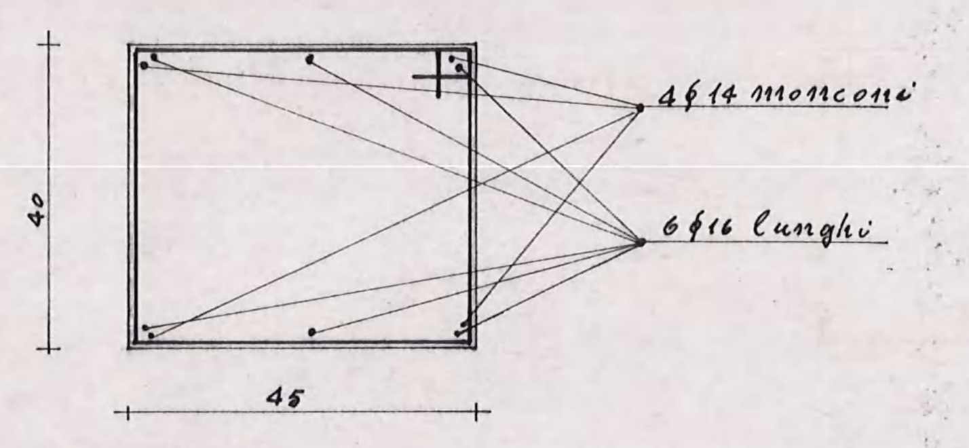
40
45
4φ14 monconi
6φ16 lunghi

Staffe φ6/15"

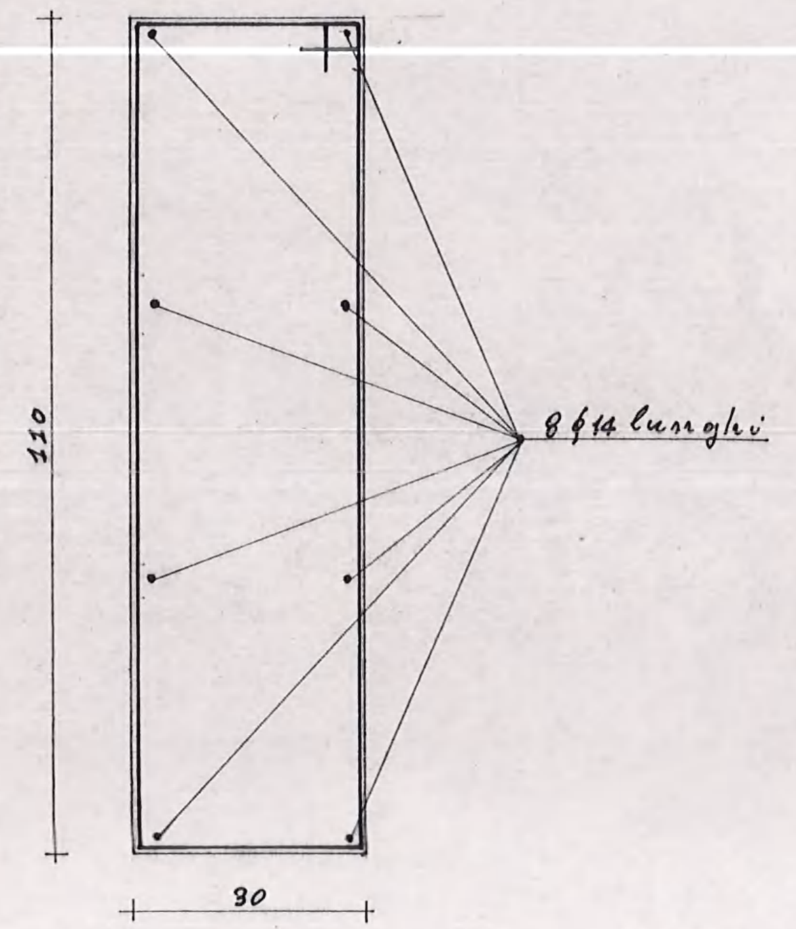
110
30
8φ14 lunghi

Staffe φ8/15"

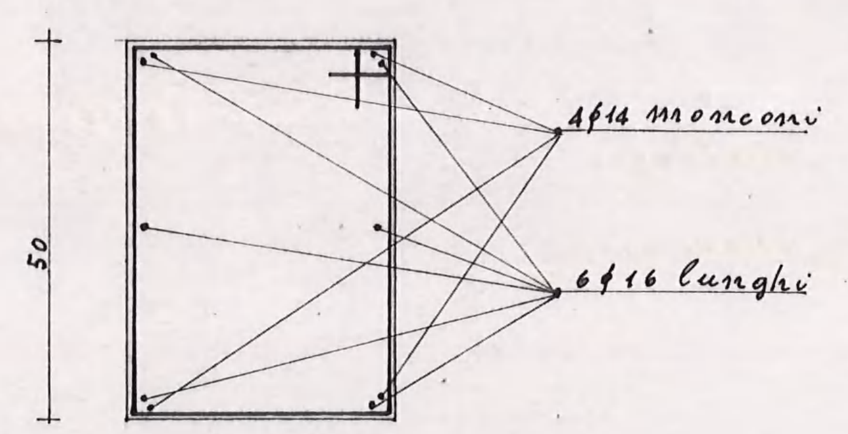
50
35
4φ14 monconi
6φ16 lunghi

Staffe φ6/15"

Pilastri III° Ordine

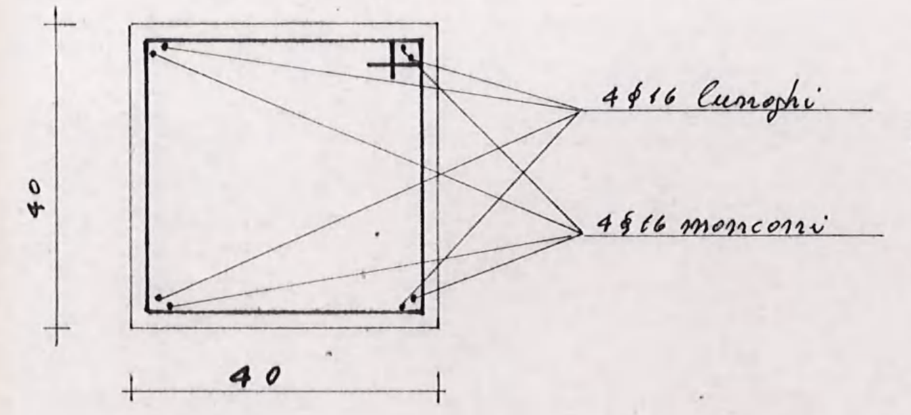
40
40
4φ16 lunghi
4φ16 monconi

Pilastri 1-2-3-4-5-6-7-8-17-24

Staffe φ6/15"

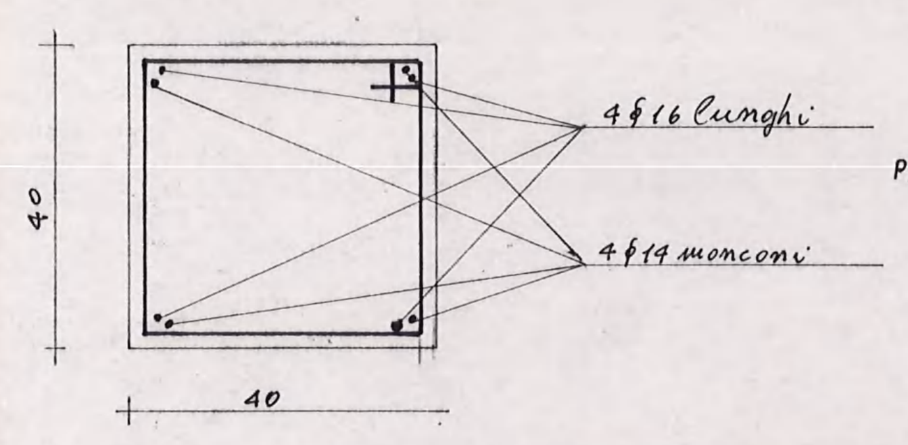
40
40
4φ16 lunghi
4φ14 monconi

Pilastri 19-22'-25-27-28-31-32-33

Staffe φ6/15"

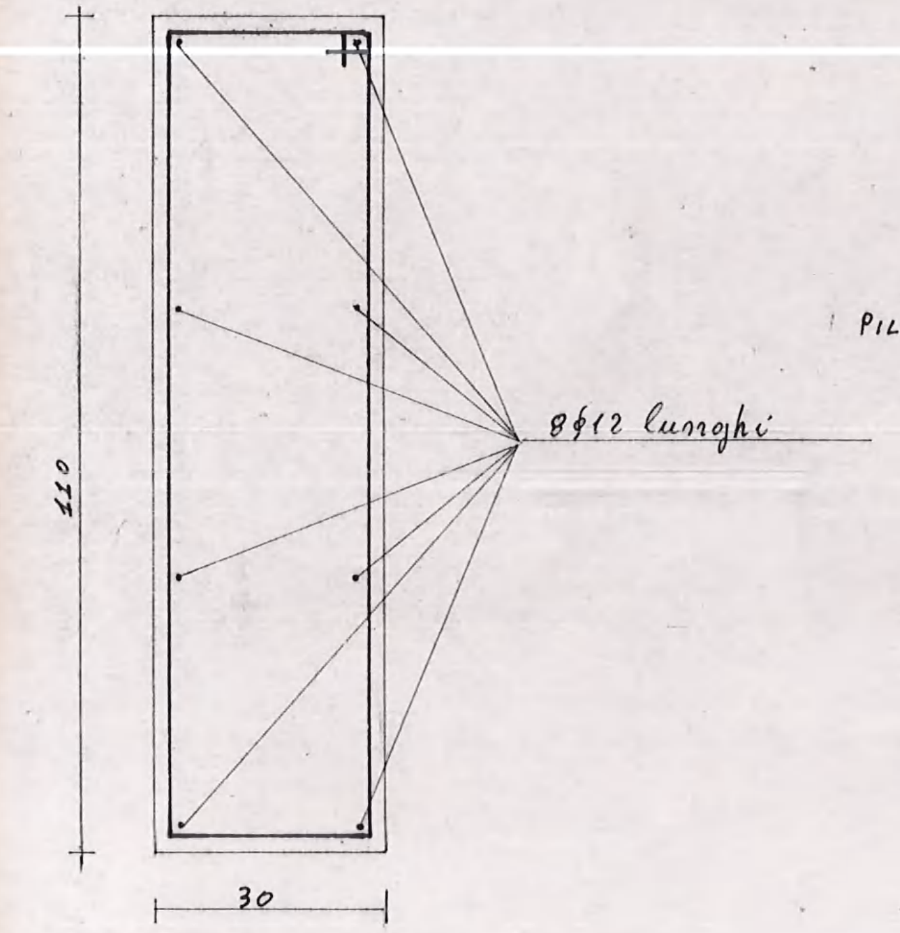
110
30
8φ12 lunghi

Pilastri 18-23-30

Staffe φ8/15"

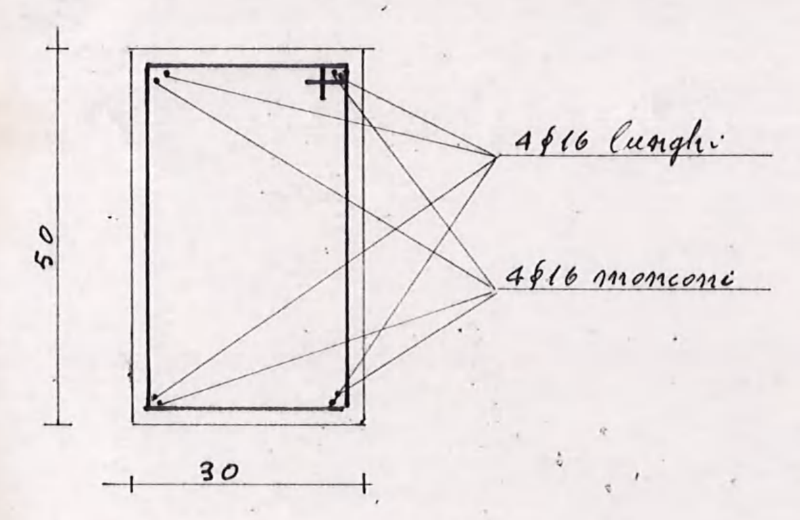
50
30
4φ16 lunghi
4φ16 monconi

Pilastri 10-12-13-15-20-21-22-26-29

Staffe φ6/15"

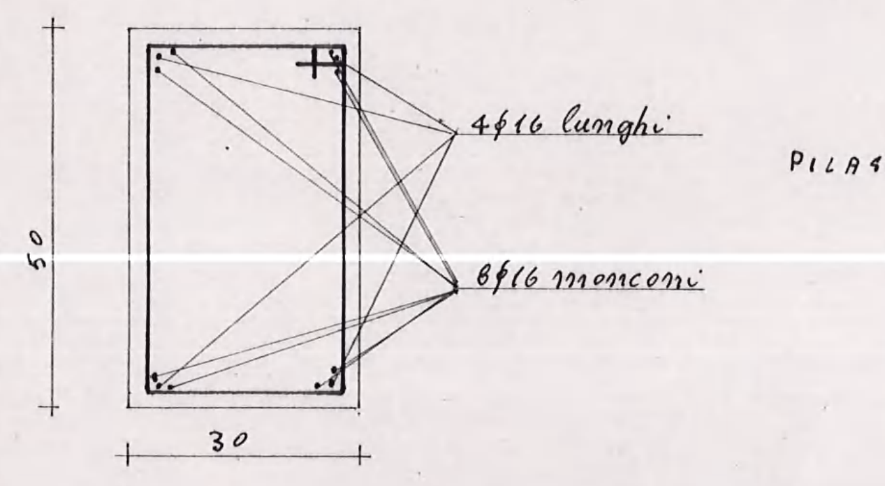
50
30
4φ16 lunghi
8φ16 monconi

Pilastro 11 - 14

Staffe φ6/15"

Pilastri IV° Ordine

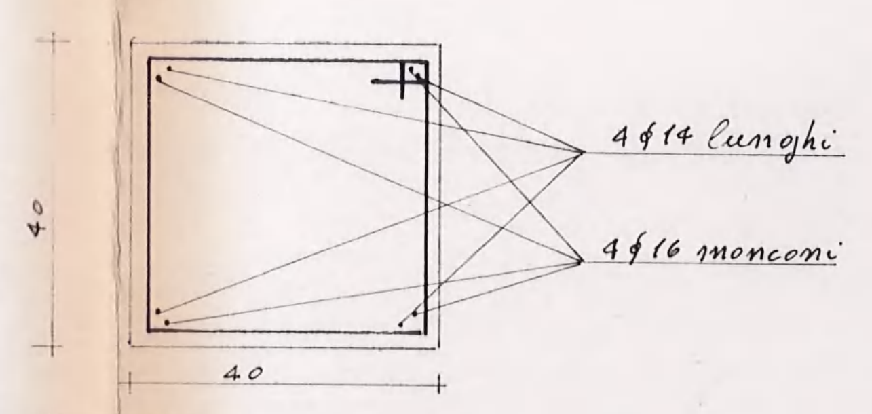
40
40
4φ14 lunghi
4φ16 monconi

Pilastri 1-2-3-4-5-6-7-8-17-19
20-22-22'-24-25-27-28-31-32-33

Staffe φ8/15"

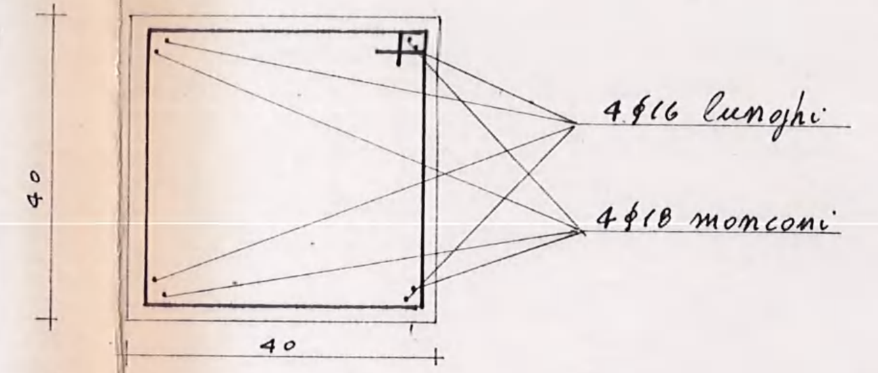
40
40
4φ16 lunghi
4φ18 monconi

Pilastri 9-16

Staffe φ6/15"

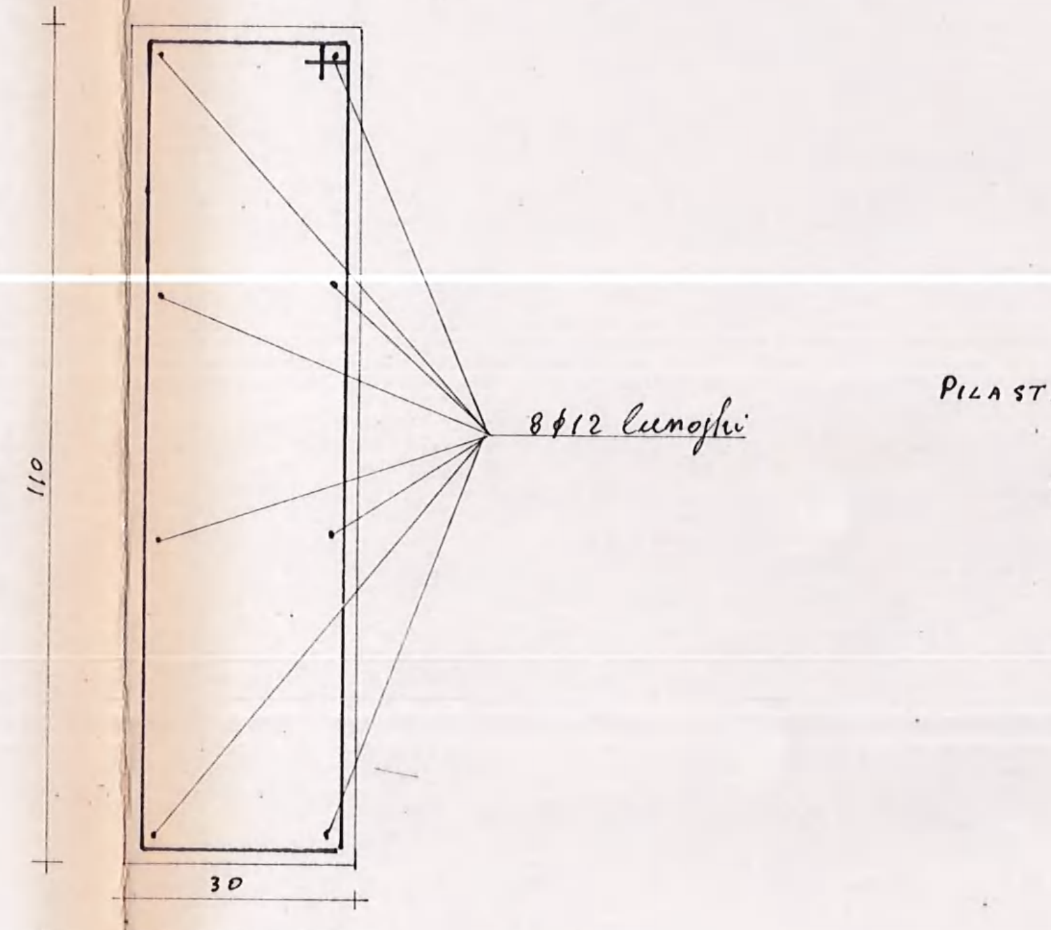
110
30
8φ12 lunghi

Pilastri 18-23-30

Staffe φ8/15"

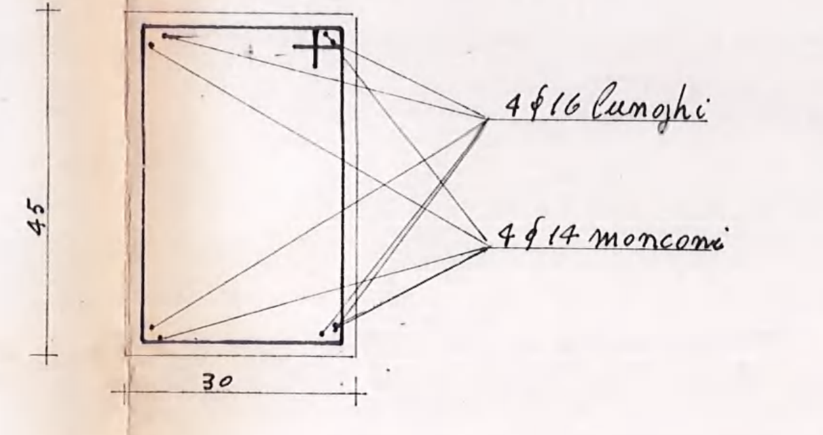
45
30
4φ16 lunghi
4φ14 monconi

Pilastri 10-12-13-15-21-26-29

Staffe φ6/15"

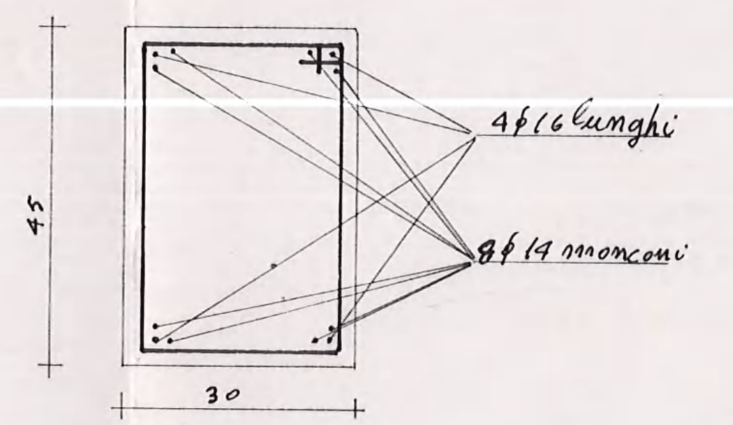
45
30
4φ16 lunghi
8φ14 monconi

Pilastri 9-16

Staffe φ6/15"

Pilastri V° Ordine

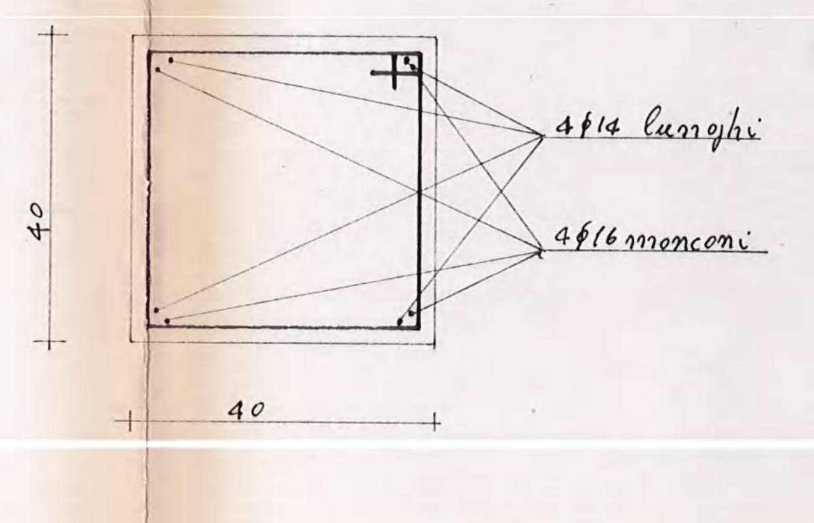
40
40
4φ14 lunghi
4φ16 monconi

Pilastri 2-3-4-5-6-7-19-20-22-22'
24-25-27-28

Staffe φ6/15"

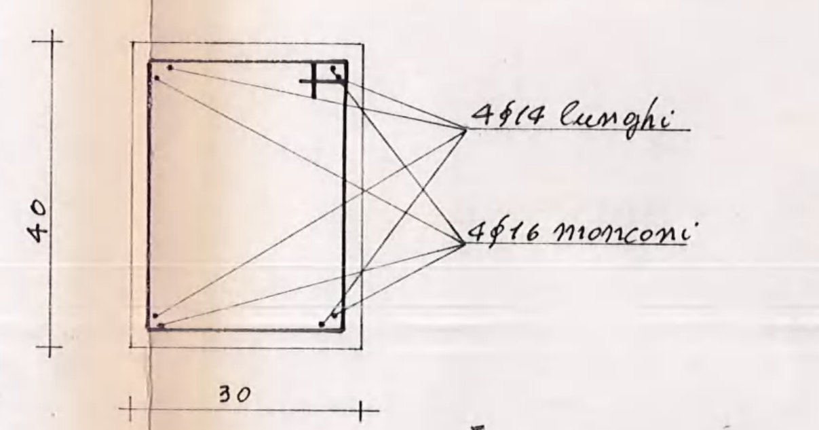
40
30
4φ14 lunghi
4φ16 monconi

Pilastri 10-11-12-13-14-15-18-21
23-26-29-30

Staffe φ6/15"